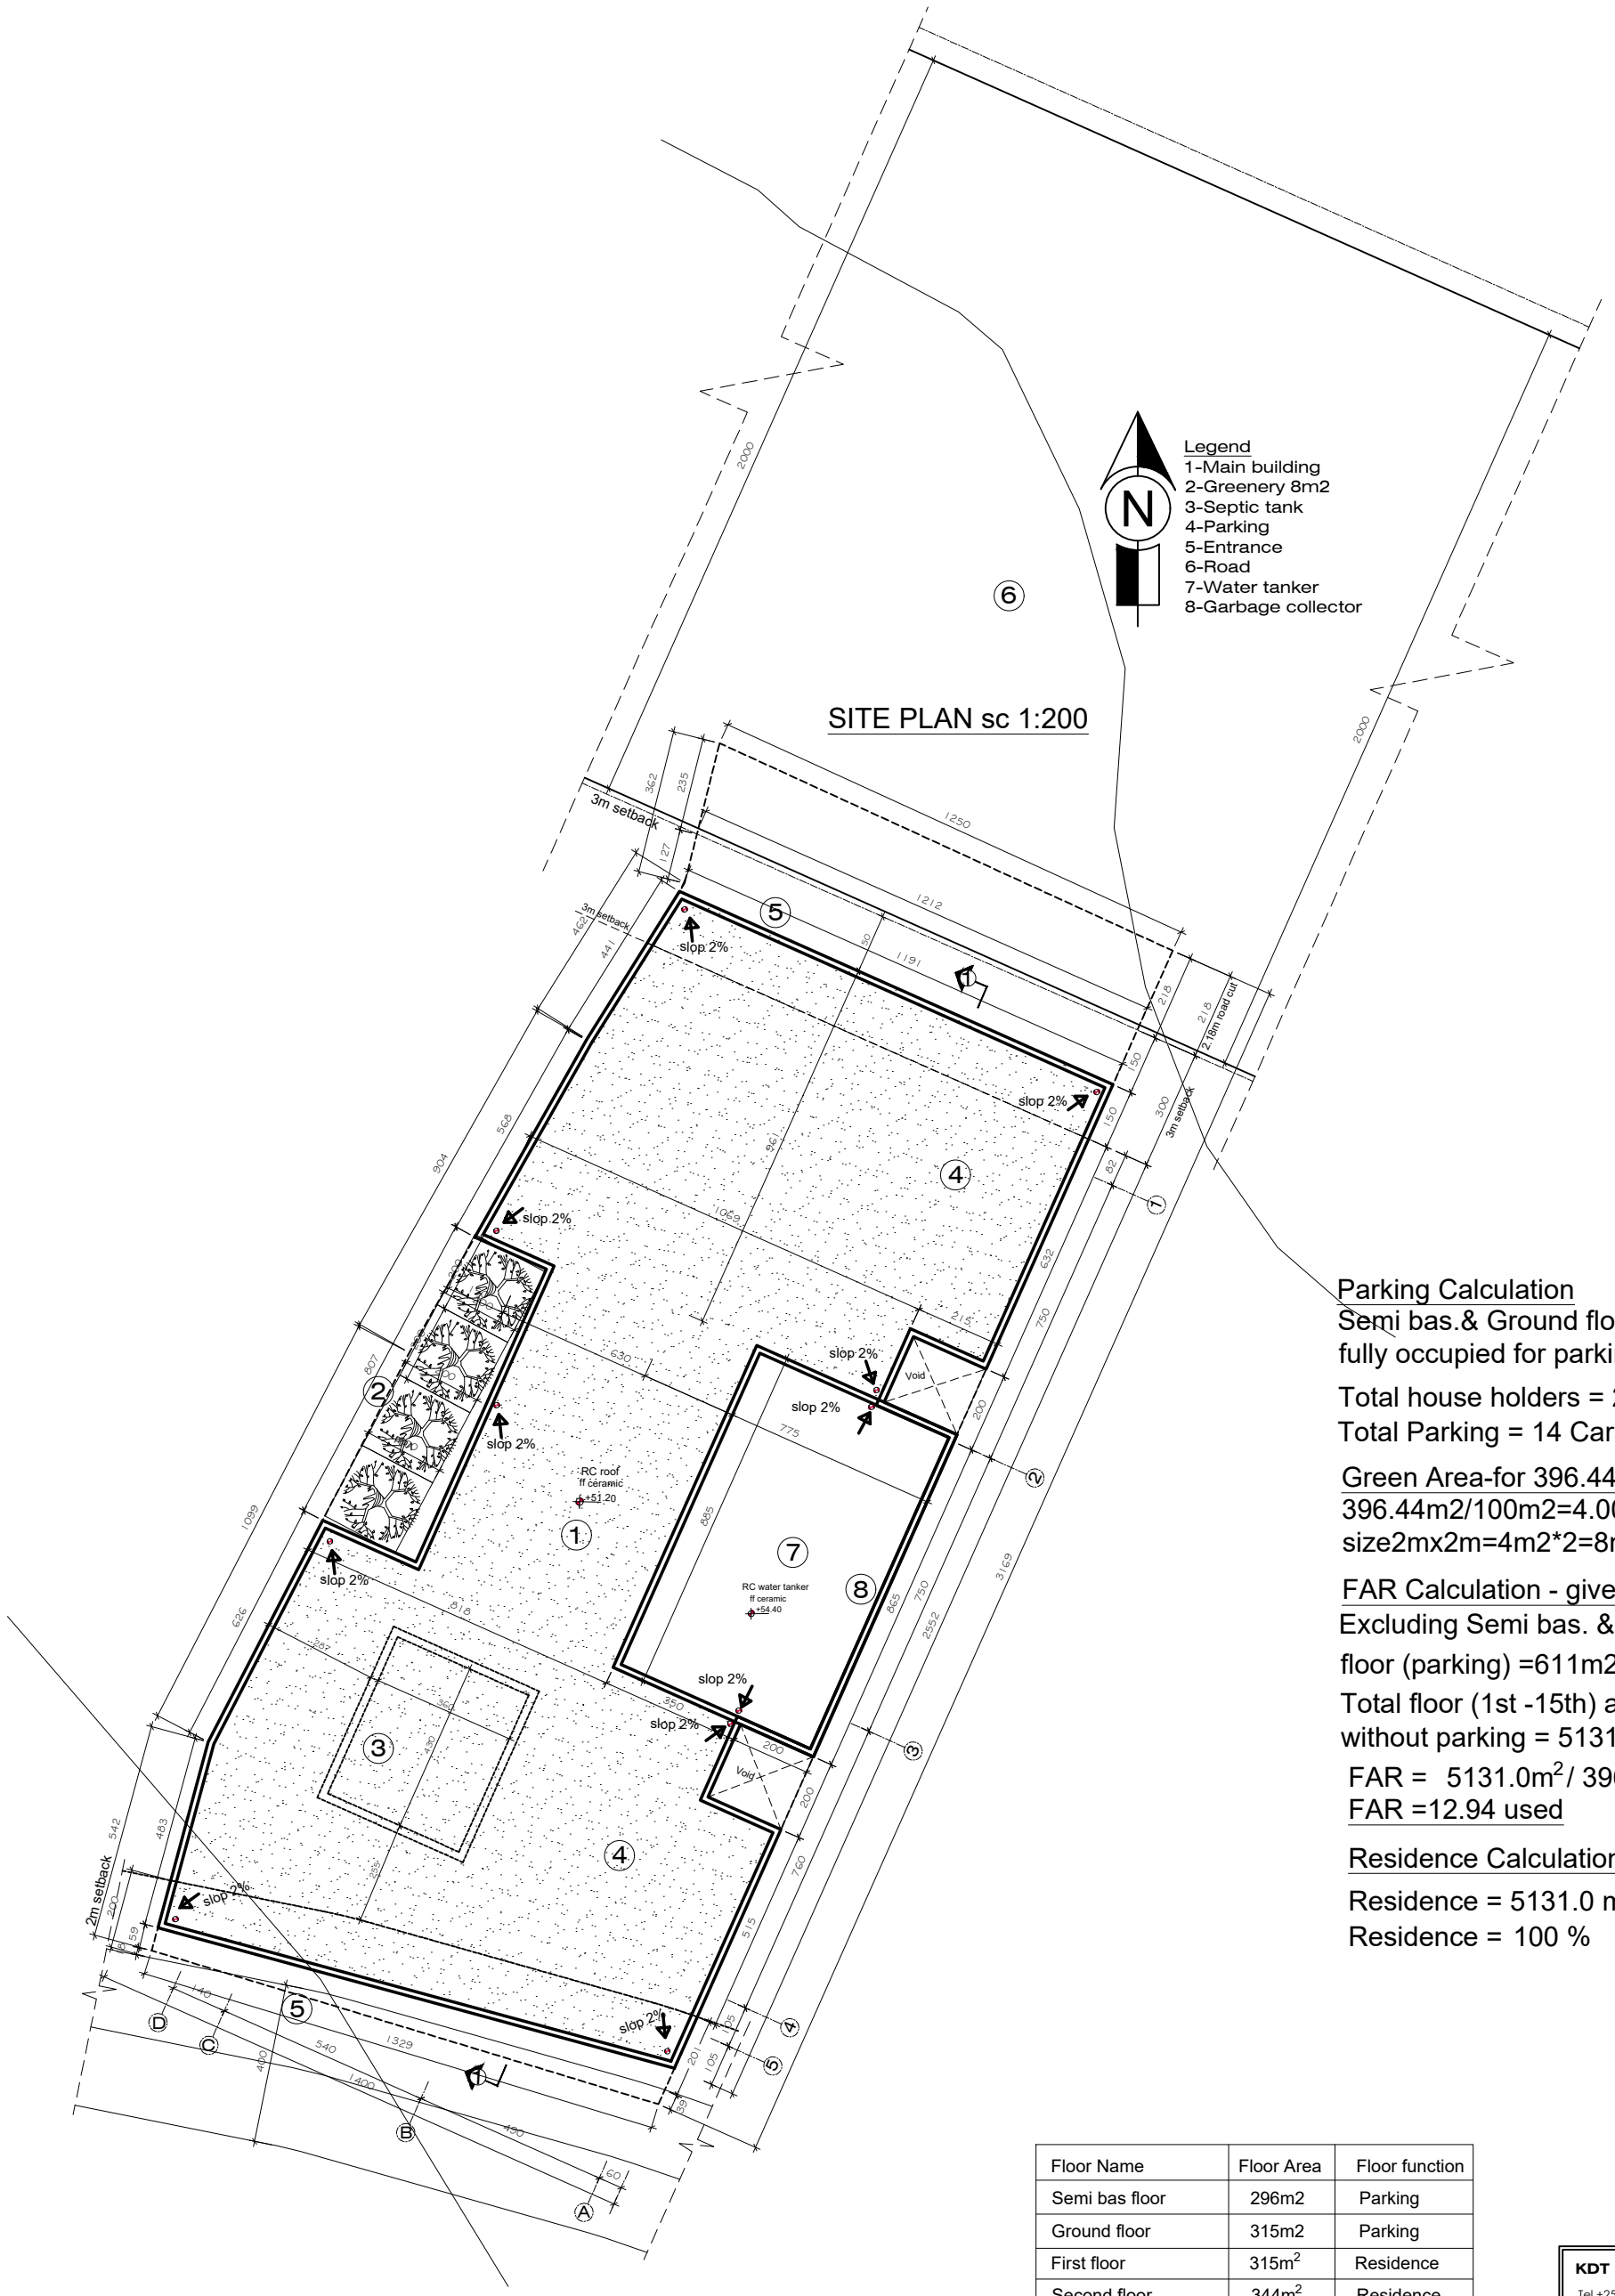


Parking Calculation

Semi bas.& Ground floor are fully occupied for parking

Total house holders = 28/2 = 14car

Total Parking = 14 Cars

Green Area-for 396.44m2 plot

396.44m2/100m2=4.00 tree

size2mx2m=4m2*2=8m2

FAR Calculation - given (2-Free) 70m bh

Excluding Semi bas. & Ground floor (parking) =611m2

Total floor (1st -15th) area without parking = 5131.0m2

FAR = 5131.0m^2 / 396.44m^2

FAR =12.94 used

Residence Calculation

Residence = 5131.0 m^2

Residence = 100 %

Floor Name	Floor Area	Floor function
Semi bas floor	296m2	Parking
Ground floor	315m2	Parking
First floor	315m^2	Residence
Second floor	344m^2	Residence
Third floor	344m^2	Residence
Fourth floor	344m^2	Residence
Fifth floor	344m^2	Residence
Sixth floor	344m^2	Residence
Seventh floor	344m^2	Residence
Eighth floor	344m^2	Residence
Ninth floor	344m^2	Residence
Tenth floor	344m^2	Residence
Eleventh floor	344m^2	Residence
Twelfth floor	344m^2	Residence
Thirteenth floor	344m^2	Residence
Fourteenth floor	344m^2	Residence
Fifteenth floor	344m^2	Residence
Grand total	5,742.00m2	

KDT DESIGN, DEVELOPMENT & TRADING PLC

Tel.+251-930-097319 ,+251-910-851364 ,+251-960-099854

Email- kdtdesign1@gmail.com

GRAY SHADE

Consulting Architects

Consulting Architects & Engineers

Tell. +251 911736607

Tell. +251 912354899

Po.Box 3209 code 1250

email. arefeaynej@gmail.com

Addis Ababa , Ethiopia

DESIGN STATUS: ✓ NEW | MODIFICATION | AS-BUILT | CON.


PROJECT: SB+G+15 APARTMENT BLDG

OWNER: YO HART TRADING PLC

LOCATION: City, A.A, Subcity Yeka, Kebele , Woreda 08, House No
Title deed - AA000050802441 Parcel No. Area 422m²

DWG TTL: SITE PLAN		FILE NAME: 1098	AR
DESIGN BY: AREFEAYNE B. PPAR 3208	CHECK: A.B	DRW: Medhin W.	WORKING
	SCALE: AS INDICATED	DATE: SEP 2025	DR.NO.: 01/11

SEMI BASEMENT FLOOR PLAN AT LEVEL -3.20 [FA 296m²] Scale 1:50

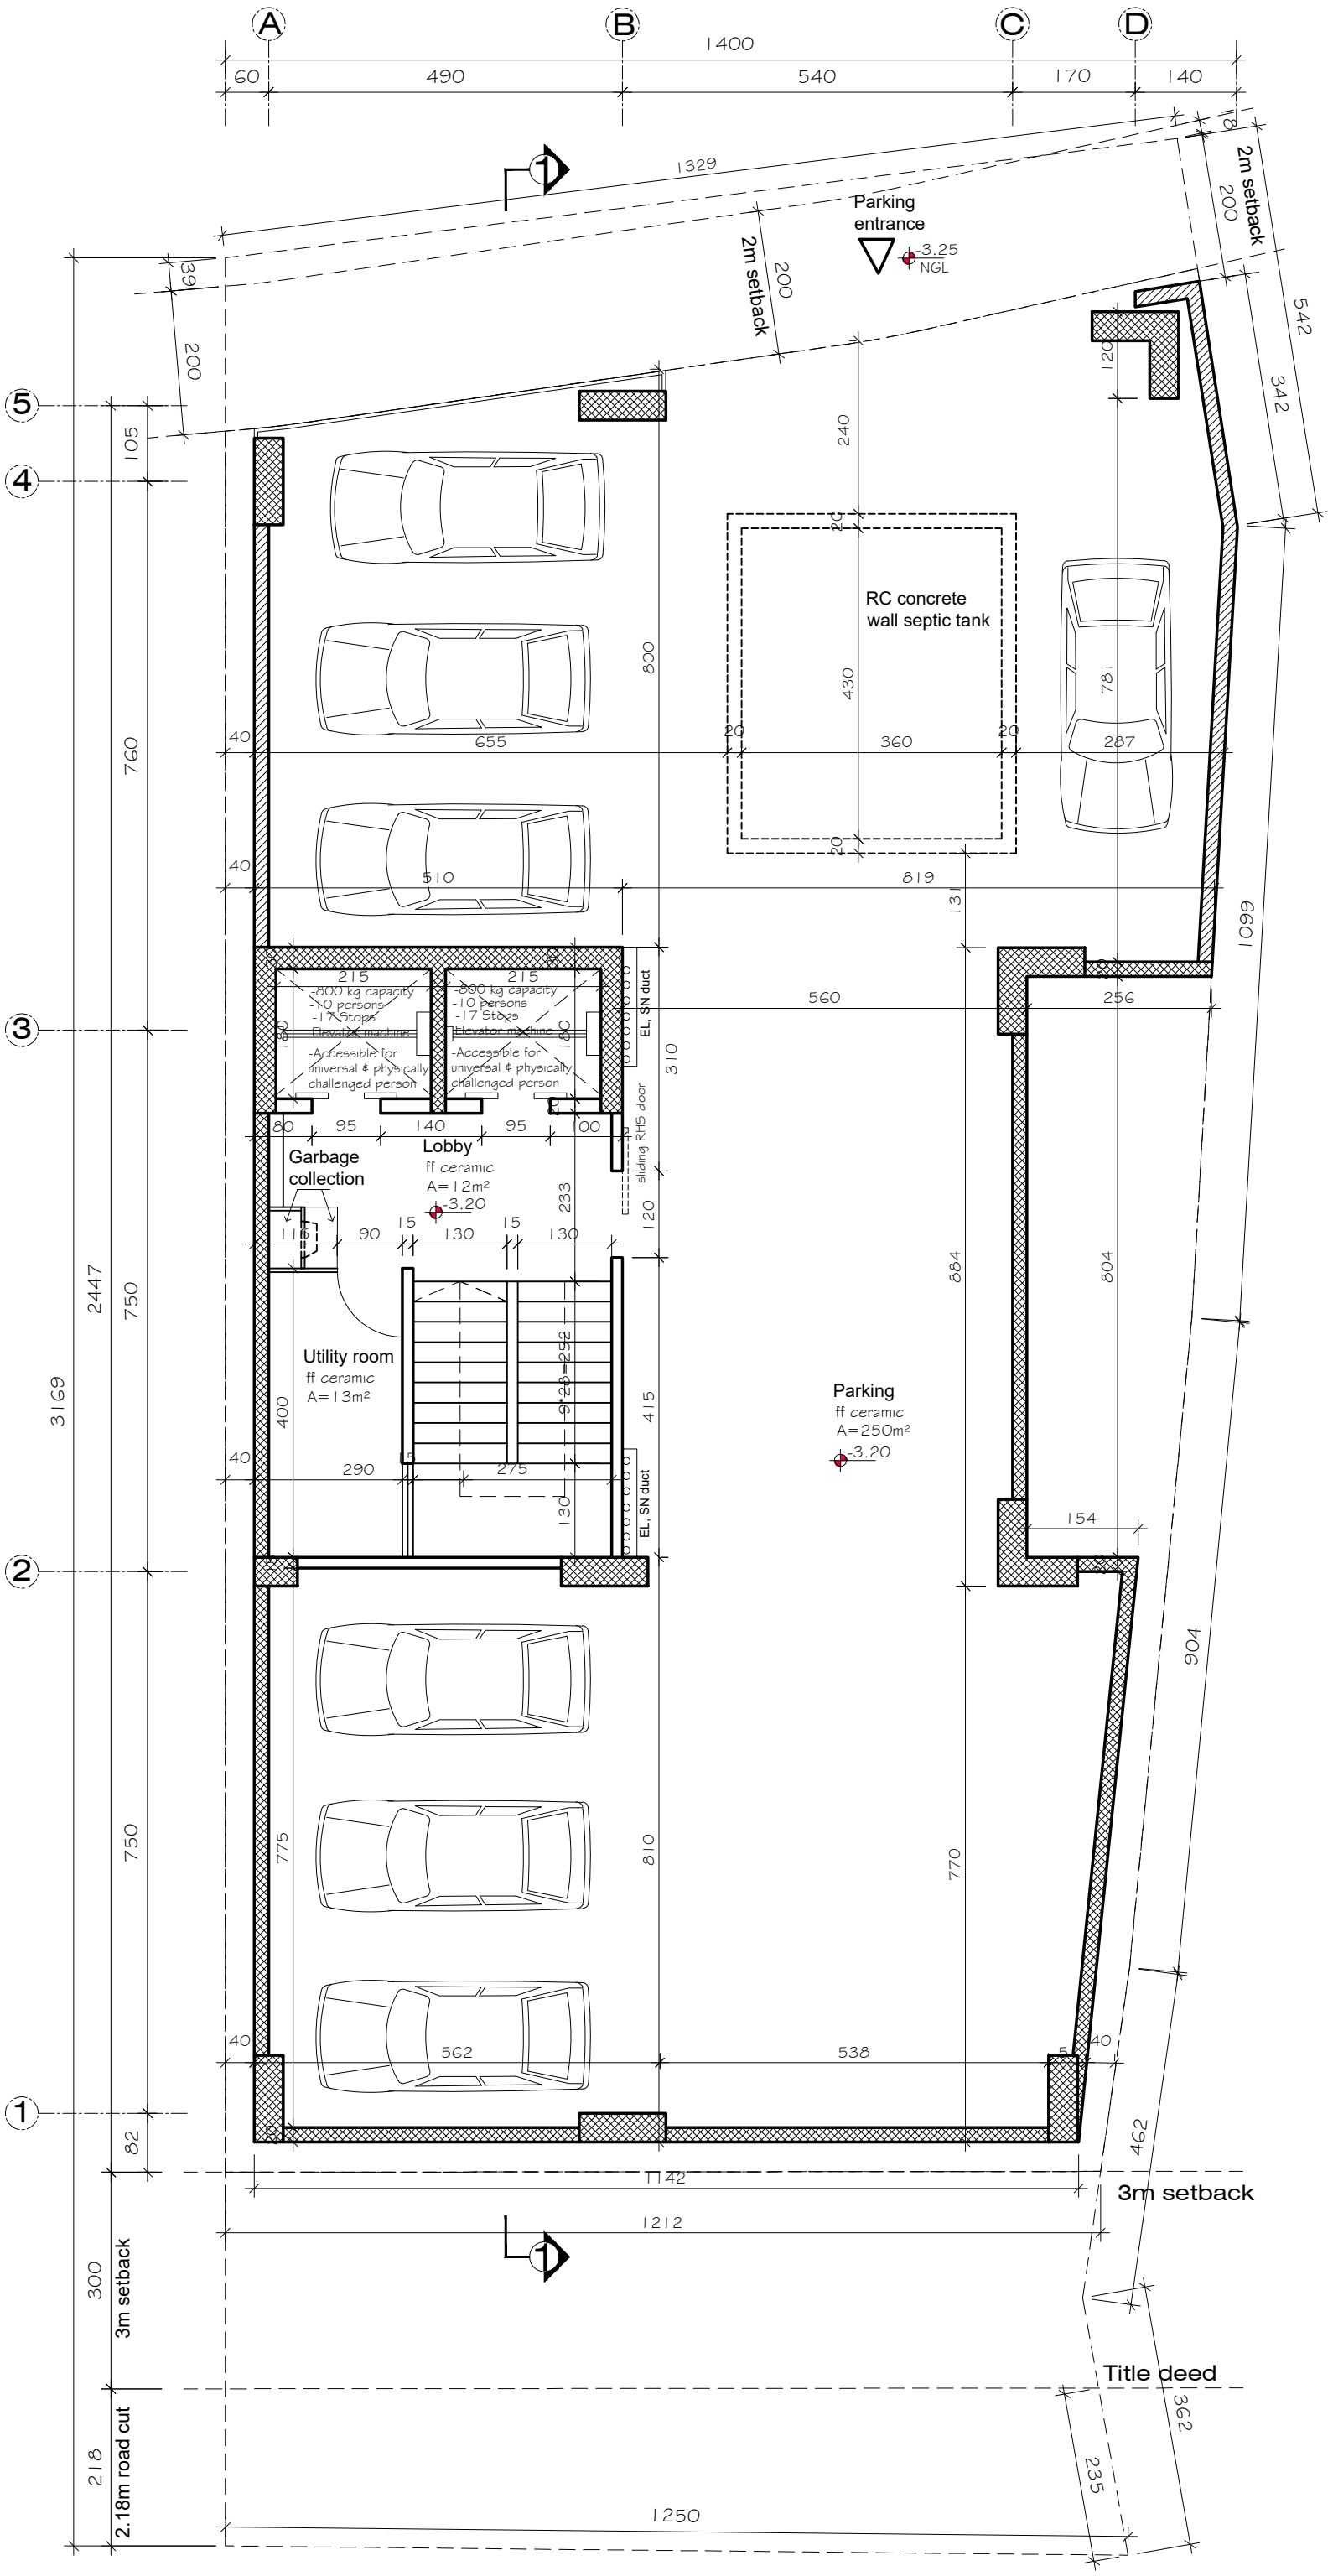

KDT DESIGN, DEVELOPMENT & TRADING PLC

Tel.+251-930-097319 ,+251-910-851364 ,+251-960-099854
Email- kdtdesign1@gmail.com

GRAY SHADE
Consulting Architects
Consulting Architects & Engineers

Tell. +251 911736607
Tell. +251 912354899
Po.Box 3209 code 1250
email. arefeaynej@gmail.com
Addis Ababa , Ethiopia

DESIGN STATUS: ✓ NEW | MODIFICATION | AS-BUILT | CON.


PROJECT: SB+G+15 APARTMENT BLDG

OWNER: YO HART TRADING PLC

LOCATION: City, A.A, Subcity Yeka, Kebele , Woreda 08, House No
Title deed - AA000050802441 Parcel No. Area 422m²

DWG TTL		FILE NAME	
SEMI BASEMENT FLOOR PLAN		1098	AR
DESIGN BY	CHECK	DRW	
AREFEAYNE B. PPAR 3208	A.B	Medhin W.	WORKING
	SCALE: AS INDICATED	DATE: SEP 2025	DR.NO.: 02/11

GROUND FLOOR PLAN AT LEVEL ±0.00 [FA 315m²] Scale 1:50

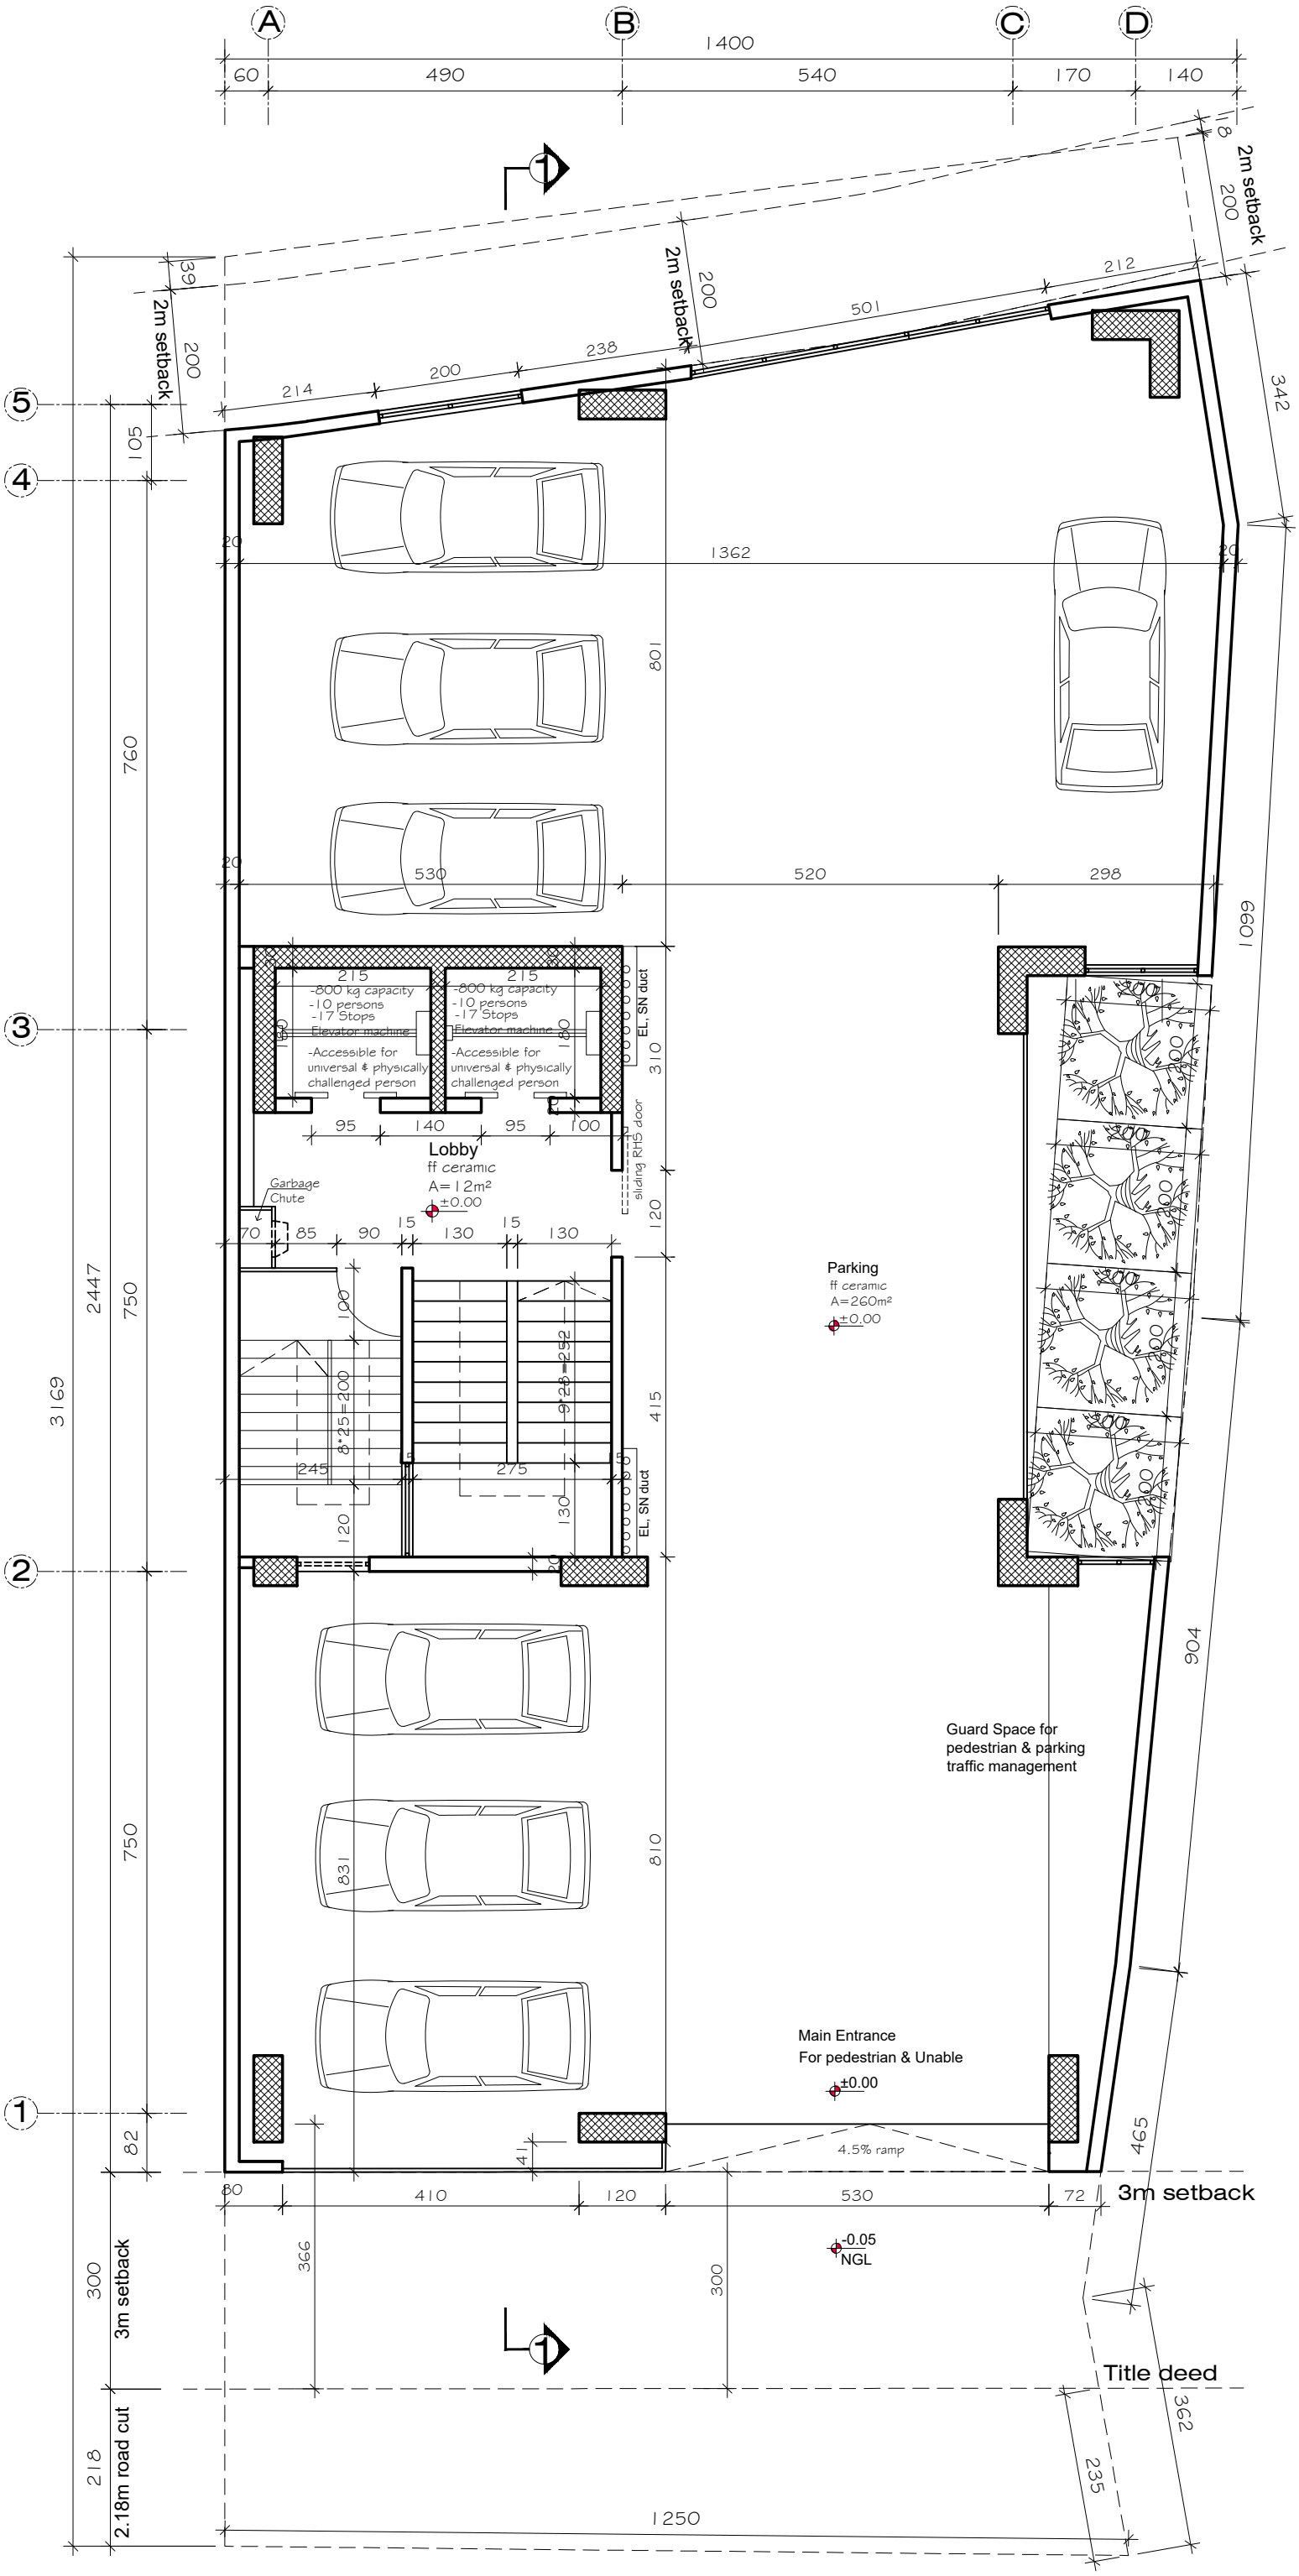

KDT DESIGN, DEVELOPMENT & TRADING PLC

Tel.+251-930-097319 ,+251-910-851364 ,+251-960-099854
Email- kdtdesign1@gmail.com

GRAY SHADE
Consulting Architects
Consulting Architects & Engineers

Tell. +251 911736607
Tell. +251 912354899
Po.Box 3209 code 1250
email. arefeaynej@gmail.com
Addis Ababa , Ethiopia

DESIGN STATUS: ✓ NEW | MODIFICATION | AS-BUILT | CON.


PROJECT: SB+G+15 APARTMENT BLDG

OWNER: YO HART TRADING PLC

LOCATION: City, A.A, Subcity Yeka, Kebele , Woreda 08, House No
Title deed - AA000050802441 Parcel No. Area 422m²

DWG TTL: GROUND FLOOR PLAN		FILE NAME: 1098	AR
DESIGN BY: AREFEAYNE B. PPAR 3208	CHECK: A.B	DRW: Medhin W.	WORKING
	SCALE: AS INDICATED	DATE: SEP 2025	DR.NO.: 03/11

FIRST FLOOR PLAN AT LEVEL +3.20 [FA 315m²] Scale 1:50

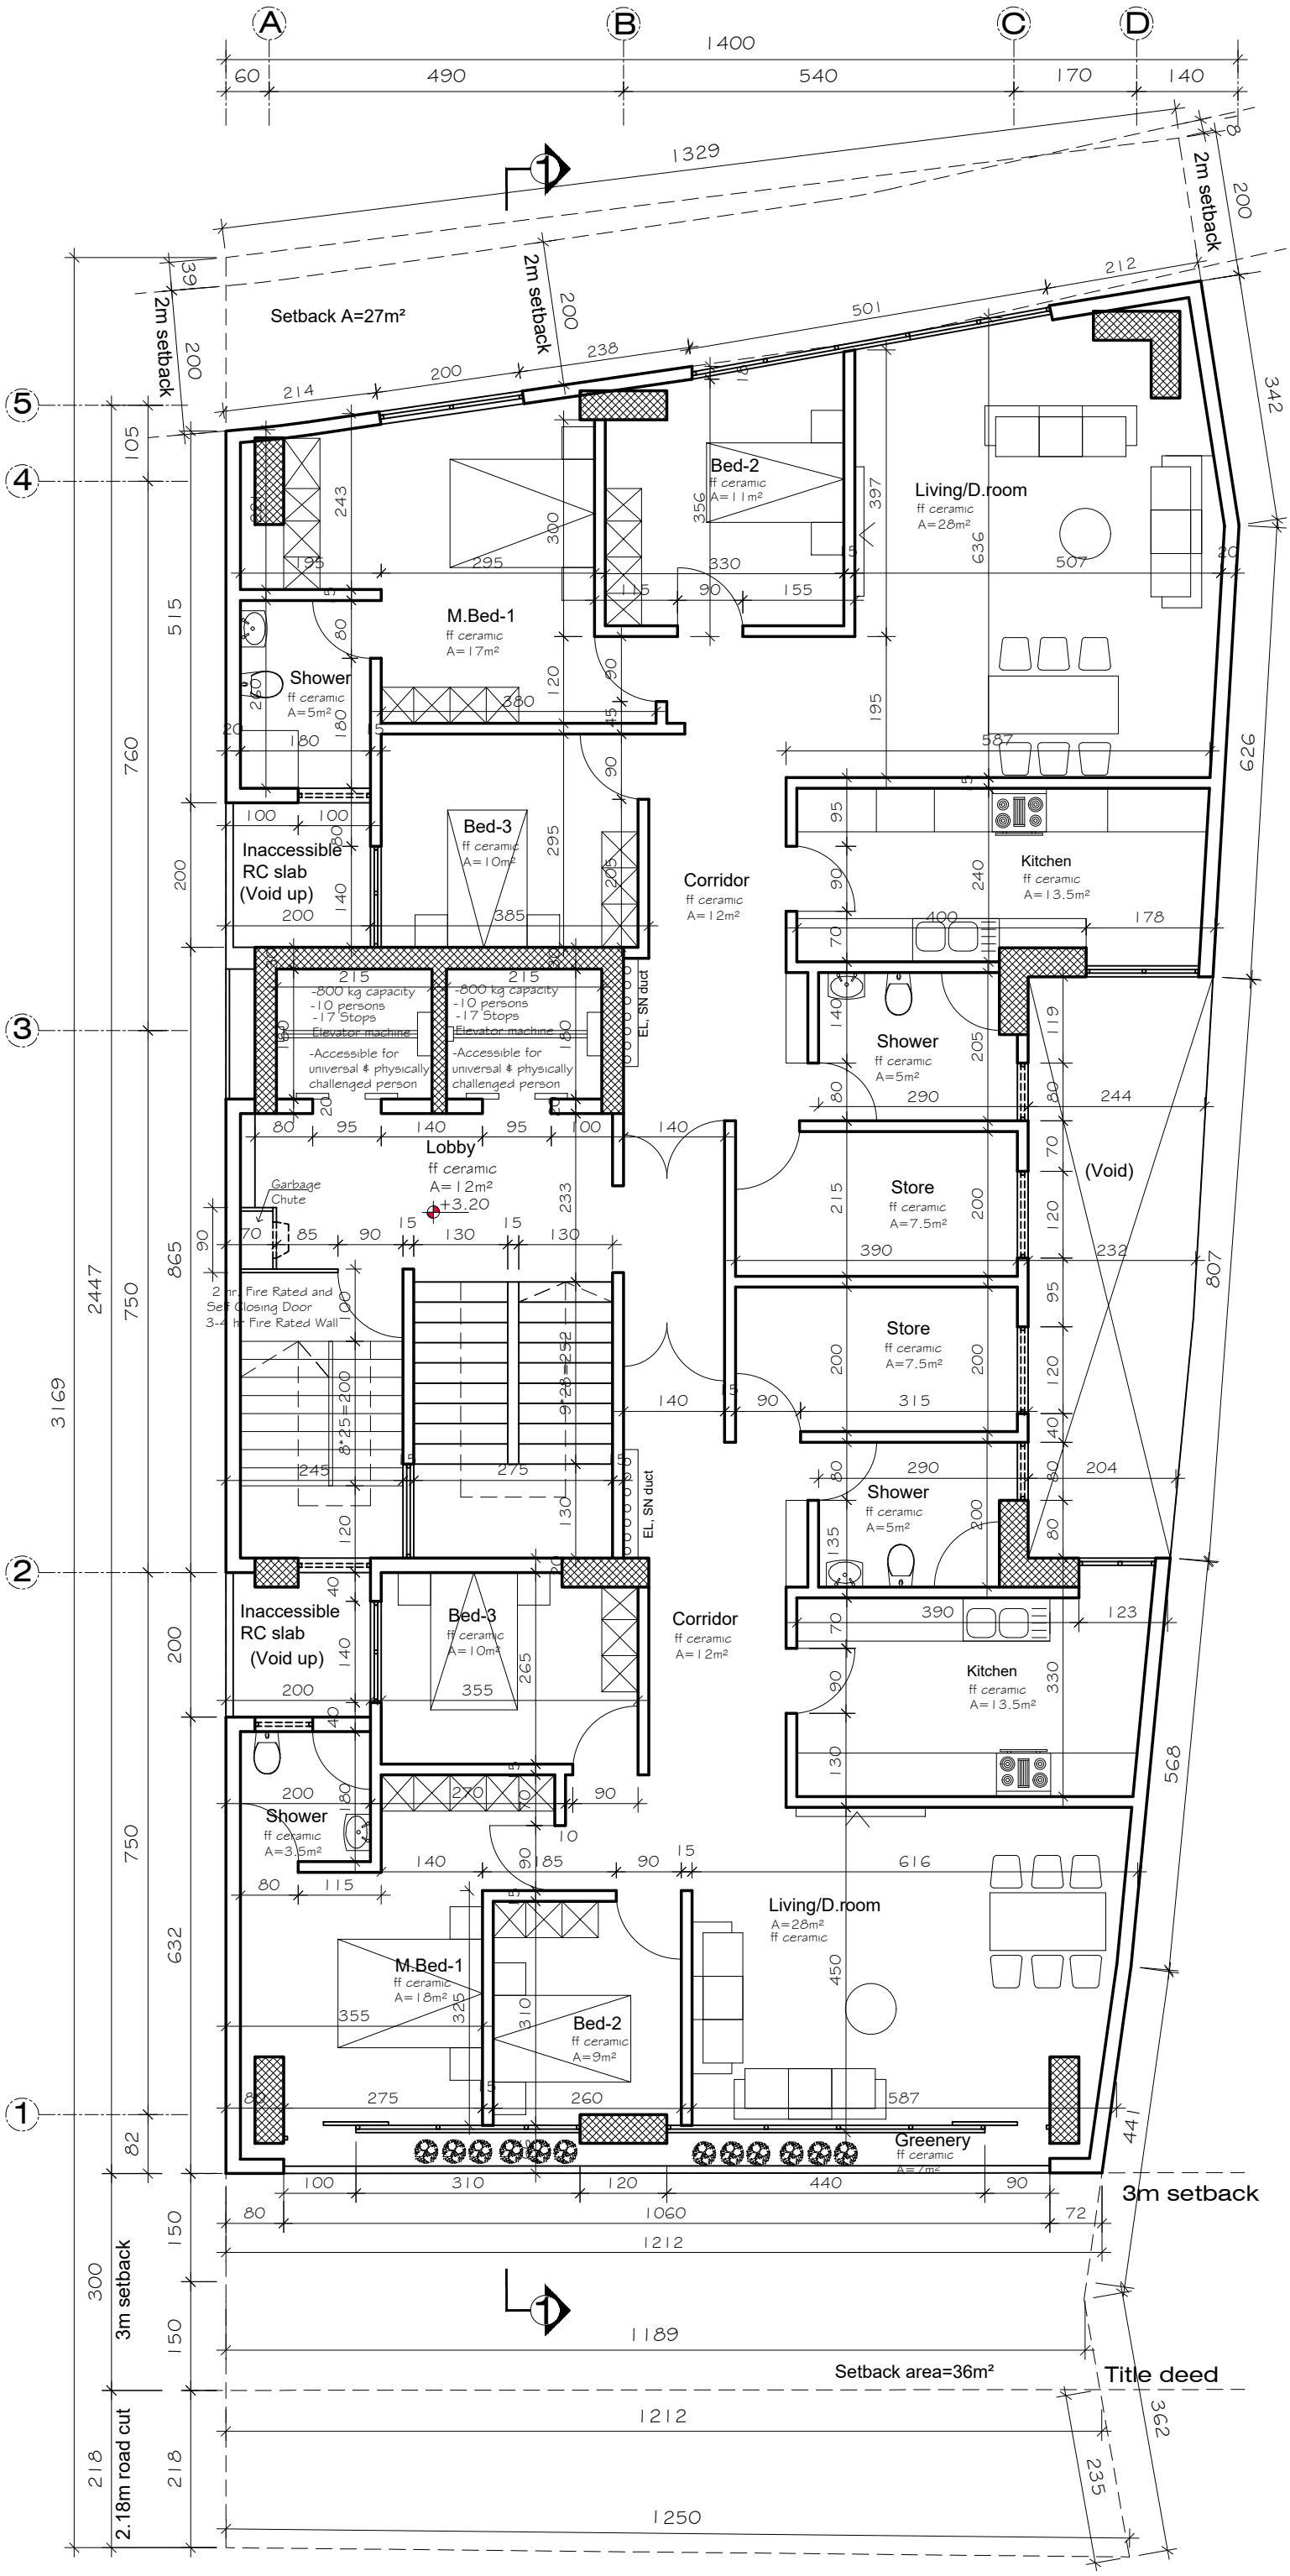

KDT DESIGN, DEVELOPMENT & TRADING PLC

Tel.+251-930-097319 ,+251-910-851364 ,+251-960-099854

Email- kdtdesign1@gmail.com

GRAY SHADE

Consulting Architects

Consulting Architects & Engineers

Tell. +251 911736607
Tell. +251 912354899
Po.Box 3209 code 1250
email. arefeaynej@gmail.com
Addis Ababa , Ethiopia

DESIGN STATUS

✓ NEW	MODIFICATION	AS-BUILT	CON.

PROJECT SB+G+15 APARTMENT BLDG


OWNER YO HART TRADING PLC

LOCATION

City, A.A, Subcity Yeka, Kebele , Woreda 08, House No
Title deed - AA000050802441 Parcel No. Area 422m²

DWG TTL	FILE NAME	
FIRST FLOOR PLAN	1098	AR
DESIGN BY: AREFEAYNE B. PPAR 3208	CHECK: A.B	DRW: Medhin W. — WORKING
	SCALE: AS INDICATED	DATE: SEP 2025 — DR.NO. 04/11

2nd-13th FLOOR PLAN AT LEVEL +6.40 - +41.60 [FA 344*12=4128m²] Scale 1:50

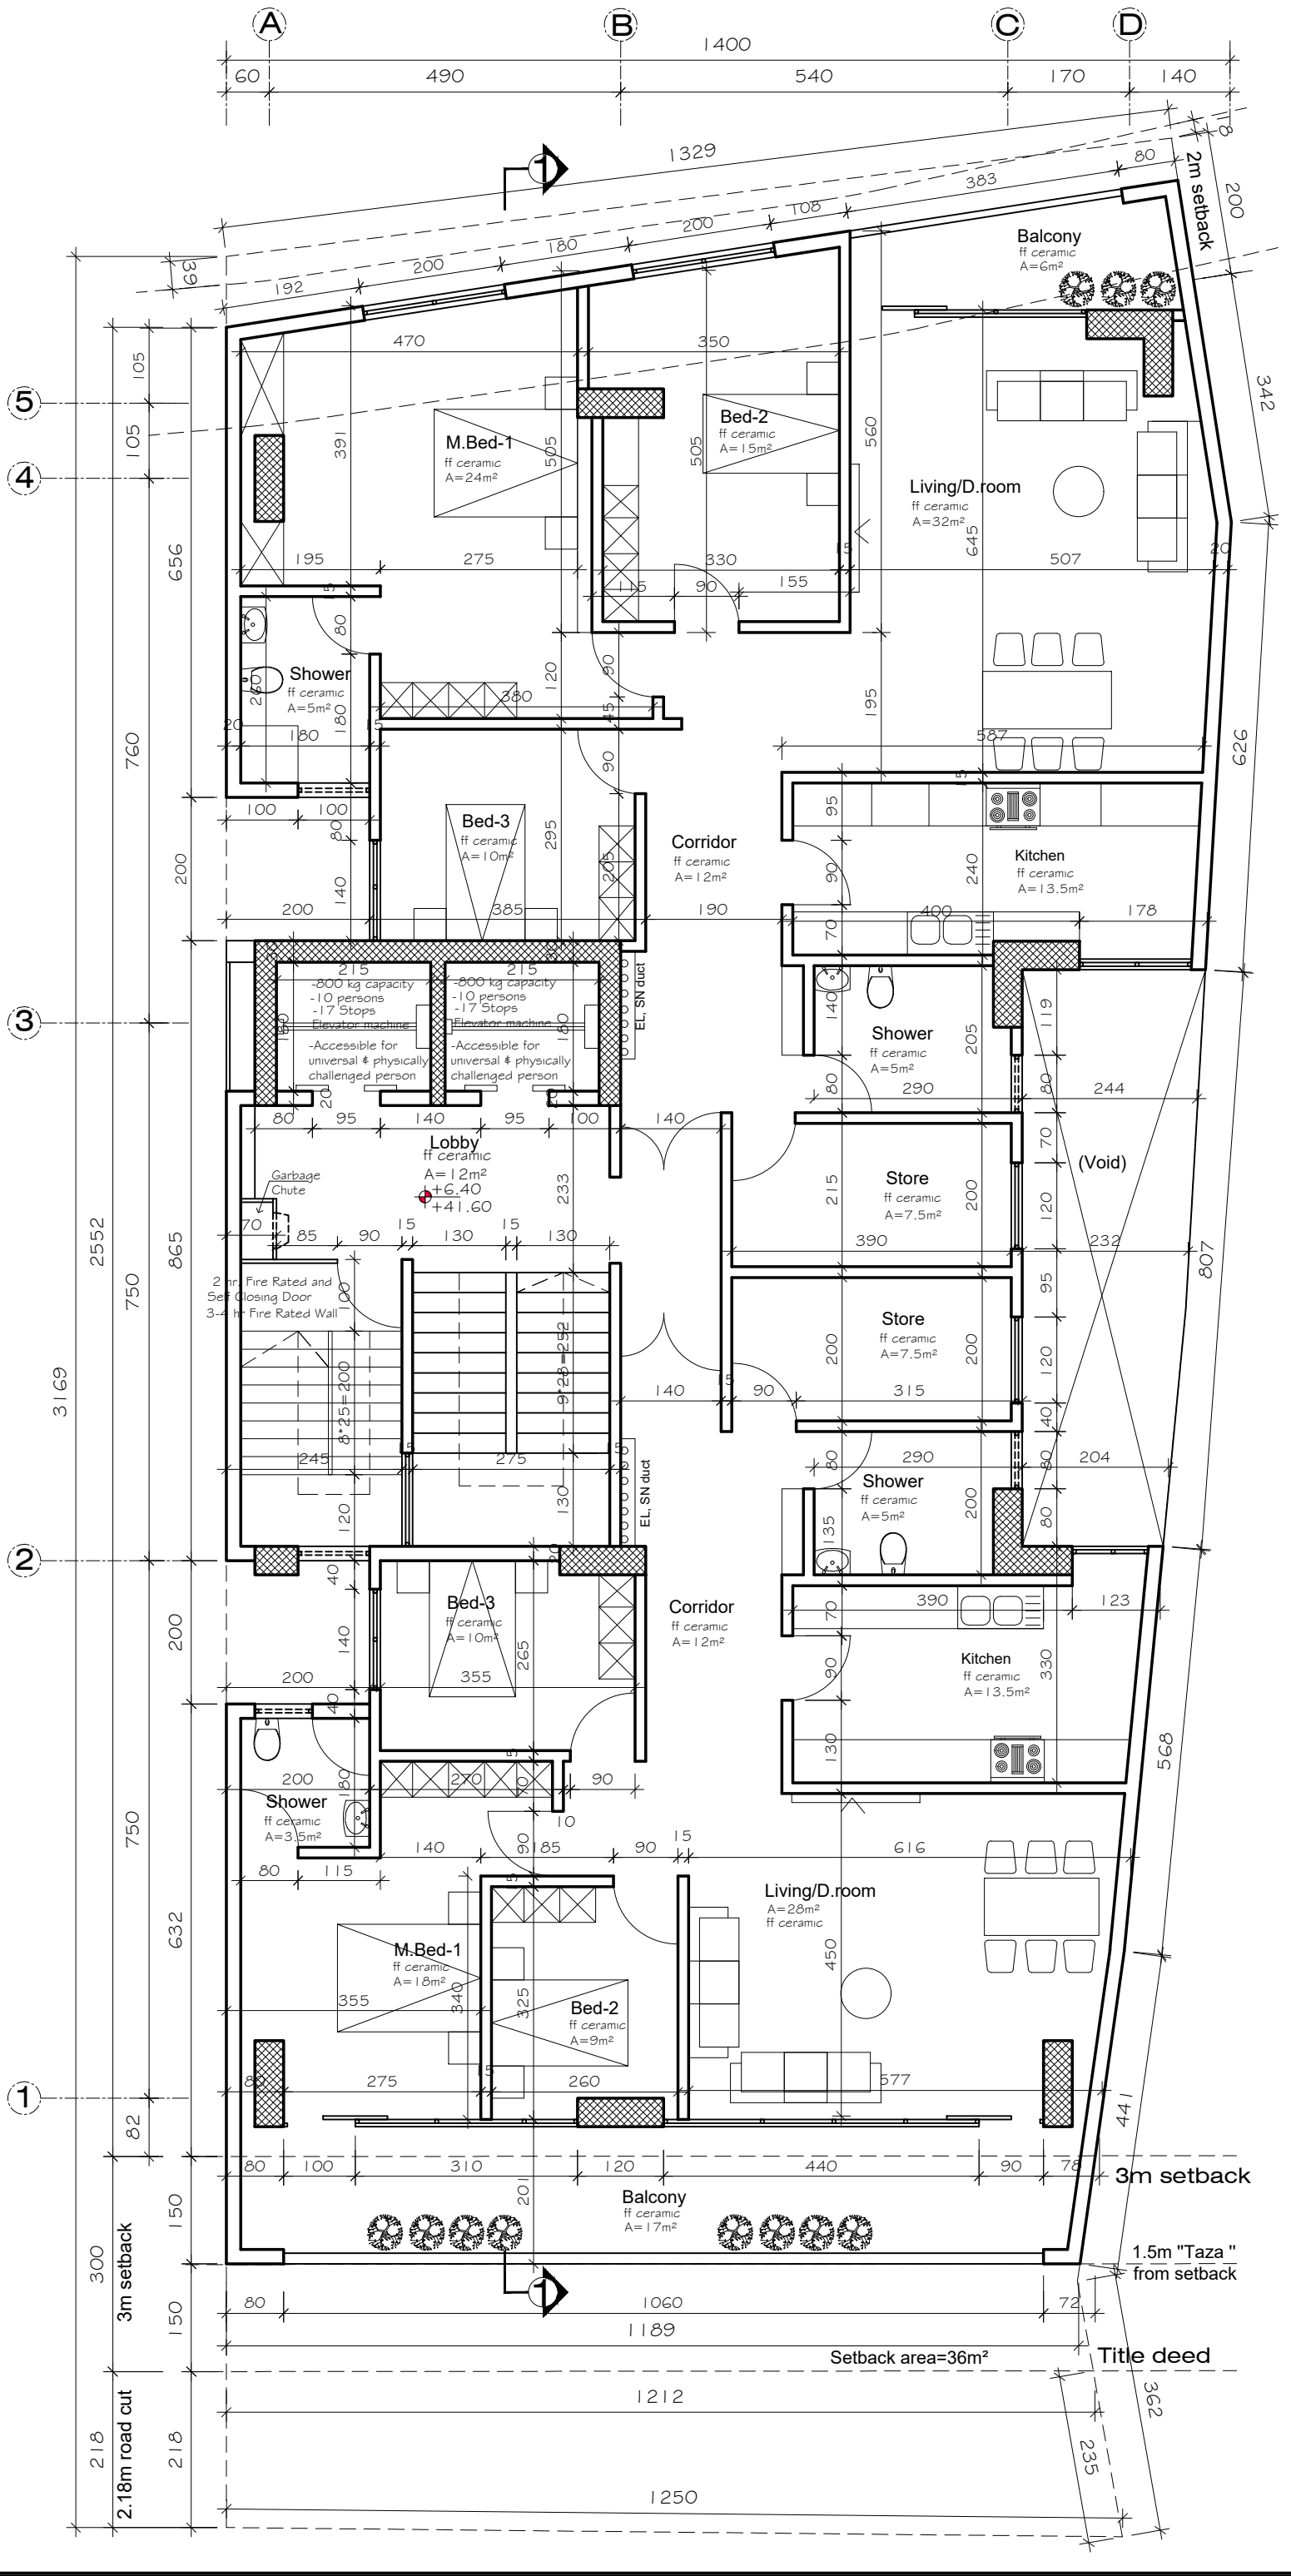

KDT DESIGN, DEVELOPMENT & TRADING PLC

Tel.+251-930-097319 ,+251-910-851364 ,+251-960-099854
Email- kdtdesign1@gmail.com

GRAY SHADE
Consulting Architects
Consulting Architects & Engineers

Tell. +251 911736607
Tell. +251 912354899
Po.Box 3209 code 1250
email. arefeaynej@gmail.com
Addis Ababa , Ethiopia

DESIGN STATUS: ✓ NEW | MODIFICATION | AS-BUILT | CON.


PROJECT: SB+G+15 APARTMENT BLDG

OWNER: YO HART TRADING PLC

LOCATION: City, A.A, Subcity Yeka, Kebele , Woreda 08, House No
Title deed - AA000050802441 Parcel No. Area 422m²

DWG TTL: TYPICAL 2nd-13th FLOOR PLAN		FILE NAME: 1098	AR
DESIGN BY: AREFEAYNE B. PPAR 3208	CHECK: A.B	DRW: Medhin W.	WORKING
	SCALE: AS INDICATED	DATE: SEP 2025	DR.NO.: 05/11

14th & 15th FLOOR PLAN AT LEVEL +44.80 - +48.00 [FA 344*2=688m²] Scale 1:50

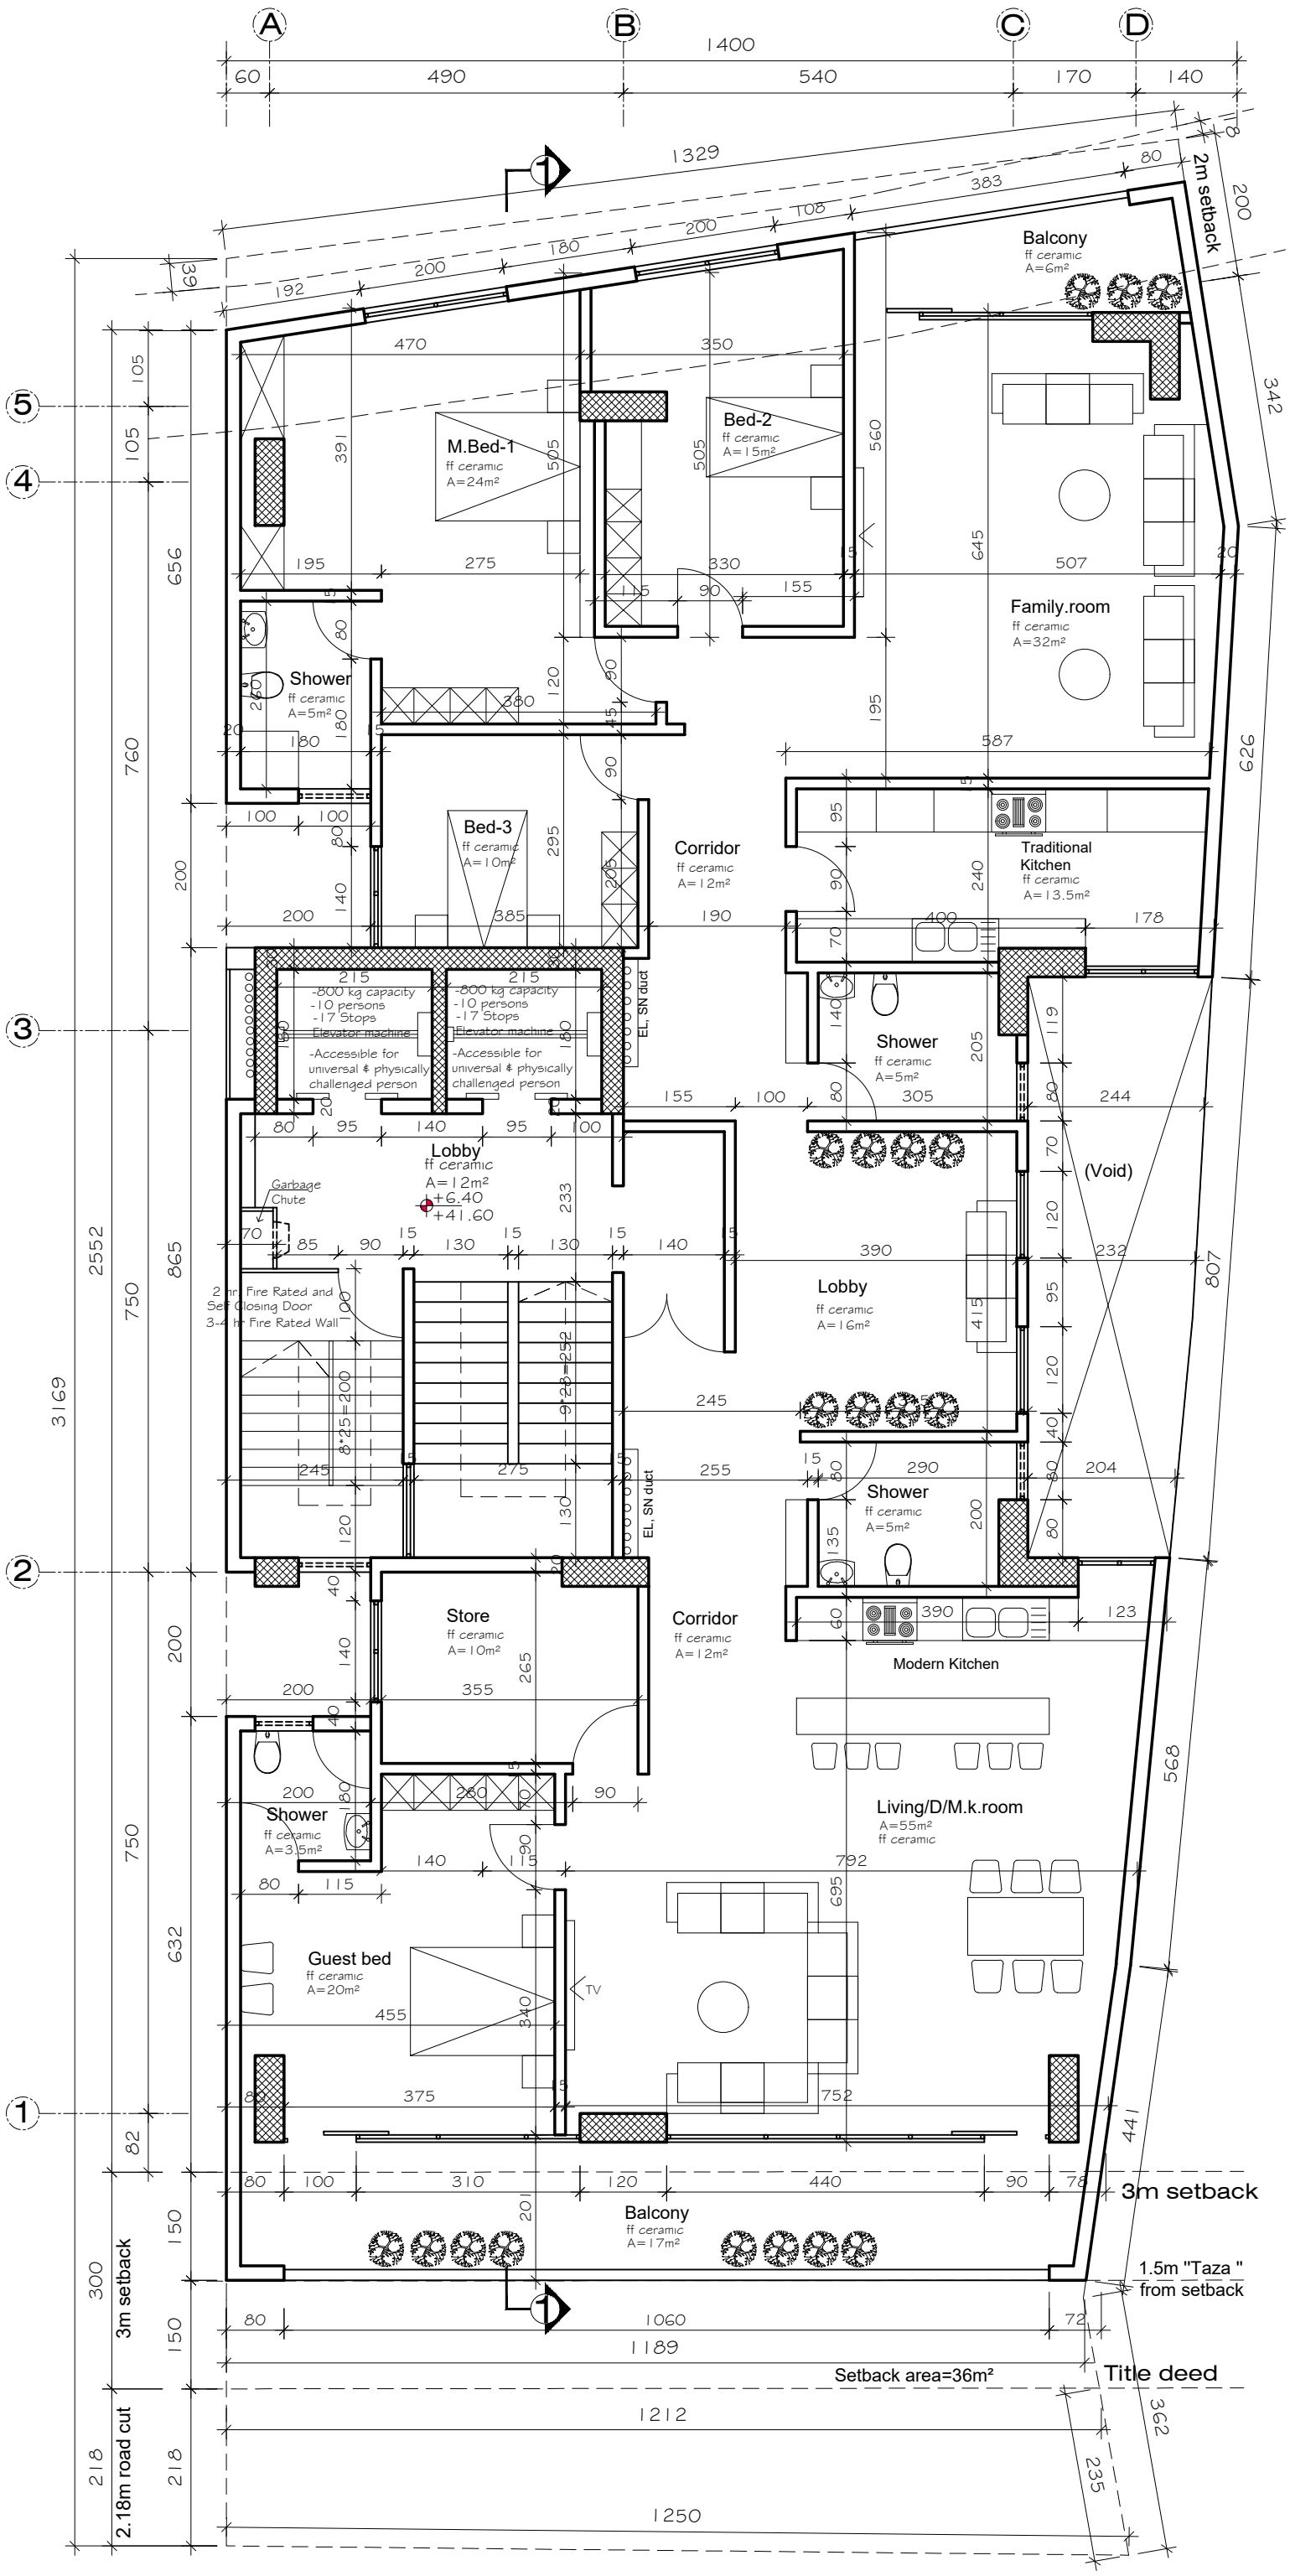

KDT DESIGN, DEVELOPMENT & TRADING PLC

Tel.+251-930-097319 ,+251-910-851364 ,+251-960-099854

Email- kdtdesign1@gmail.com

GRAY SHADE

Consulting Architects

Consulting Architects & Engineers

Tell. +251 911736607

Tell. +251 912354899

Po.Box 3209 code 1250

email. arefeaynej@gmail.com

Addis Ababa , Ethiopia

DESIGN STATUS

NEW	MODIFICATION	AS-BUILT	CON.
✓			

PROJECT SB+G+15 APARTMENT BLDG

OWNER YO HART TRADING PLC


LOCATION

City, A.A, Subcity Yeka, Kebele , Woreda 08, House No

Title deed - AA000050802441 Parcel No. Area 422m²

DWG TTL		FILE NAME	
TYPICAL 14th &15th FLOOR PLAN		1098	AR
DESIGN BY	CHECK	DRW	WORKING
AREFEAYNE B. PPAR 3208	A.B	Medhin W.	
	SCALE AS INDICATED	DATE SEP 2025	DR.NO. 06/11

RC ROOF FLOOR PLAN AT LEVEL +51.20 [FA 340m²] Scale 1:50

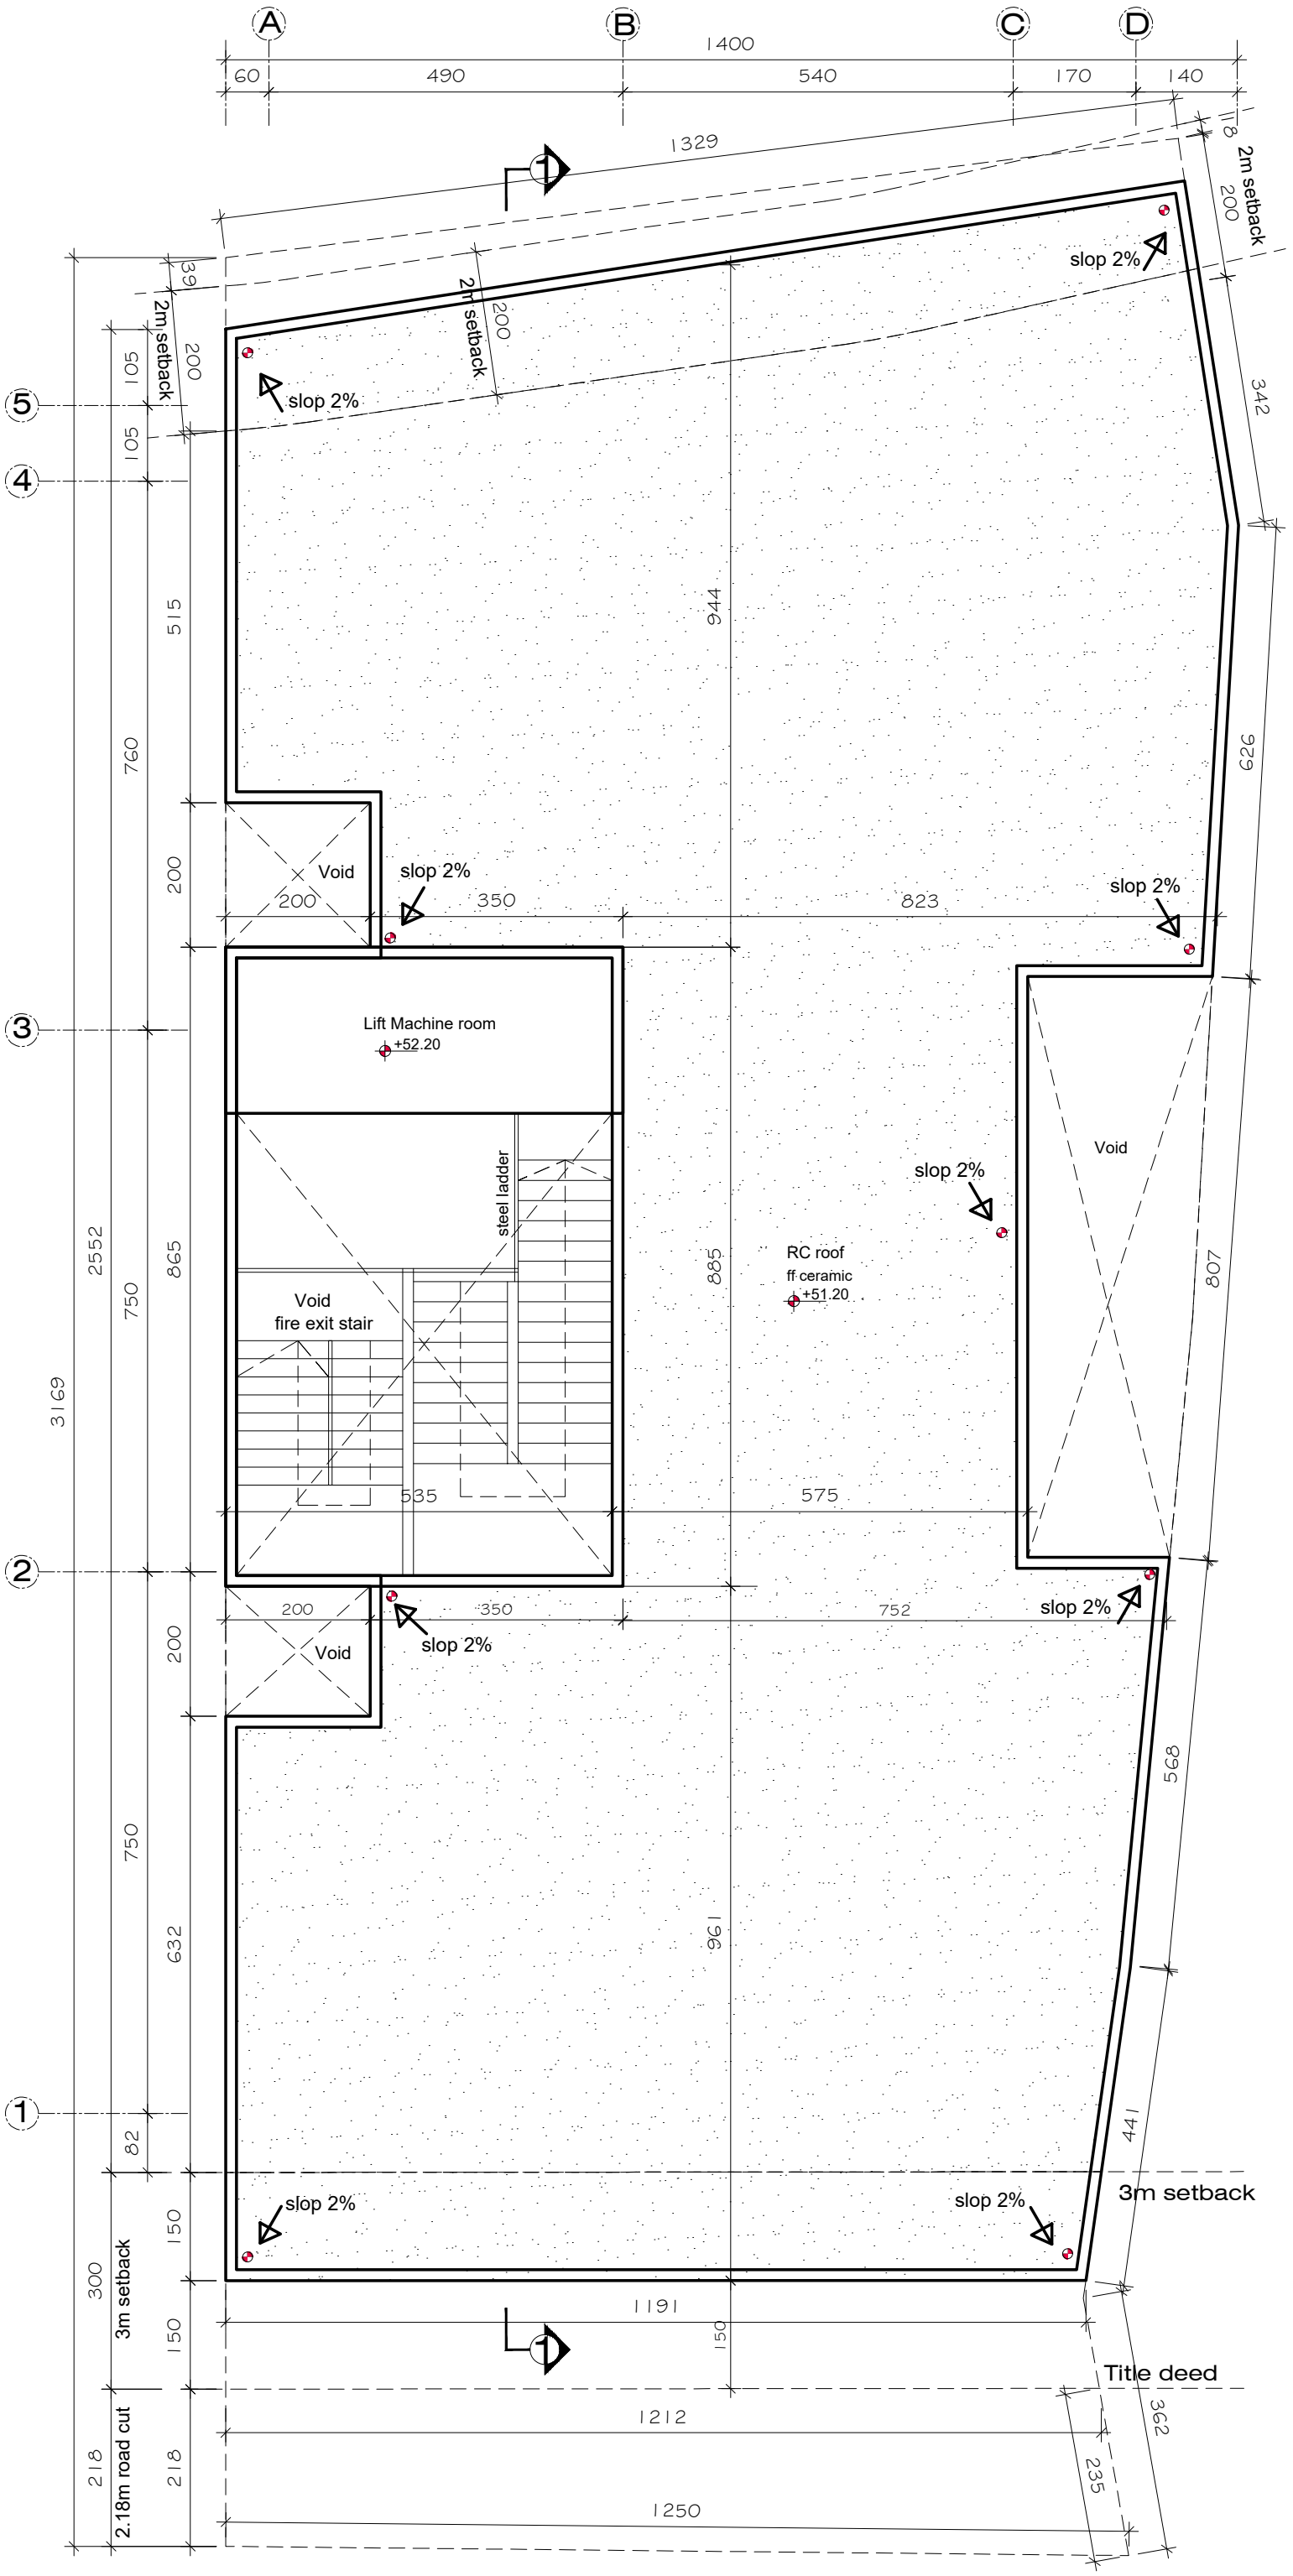

KDT DESIGN, DEVELOPMENT & TRADING PLC

Tel.+251-930-097319 ,+251-910-851364 ,+251-960-099854

Email- kdtdesign1@gmail.com

GRAY SHADE

Consulting Architects

Consulting Architects & Engineers

Tell. +251 911736607

Tell. +251 912354899

Po.Box 3209 code 1250

email. arefeaynej@gmail.com

Addis Ababa , Ethiopia

DESIGN STATUS

✓ NEW	MODIFICATION	AS-BUILT	CON.

PROJECT SB+G+15 APARTMENT BLDG


OWNER YO HART TRADING PLC

LOCATION

City, A.A, Subcity Yeka, Kebele , Woreda 08, House No

Title deed - AA000050802441 Parcel No. Area 422m²

DWG TTL		FILE NAME	
RC ROOF FLOOR PLAN		1098	**AR**
DESIGN BY	CHECK	DRW	
AREFEAYNE B. PPAR 3208	A.B	Medhin W.	WORKING
	SCALE	DATE	DR.NO.
	AS INDICATED	SEP 2025	**07/11**

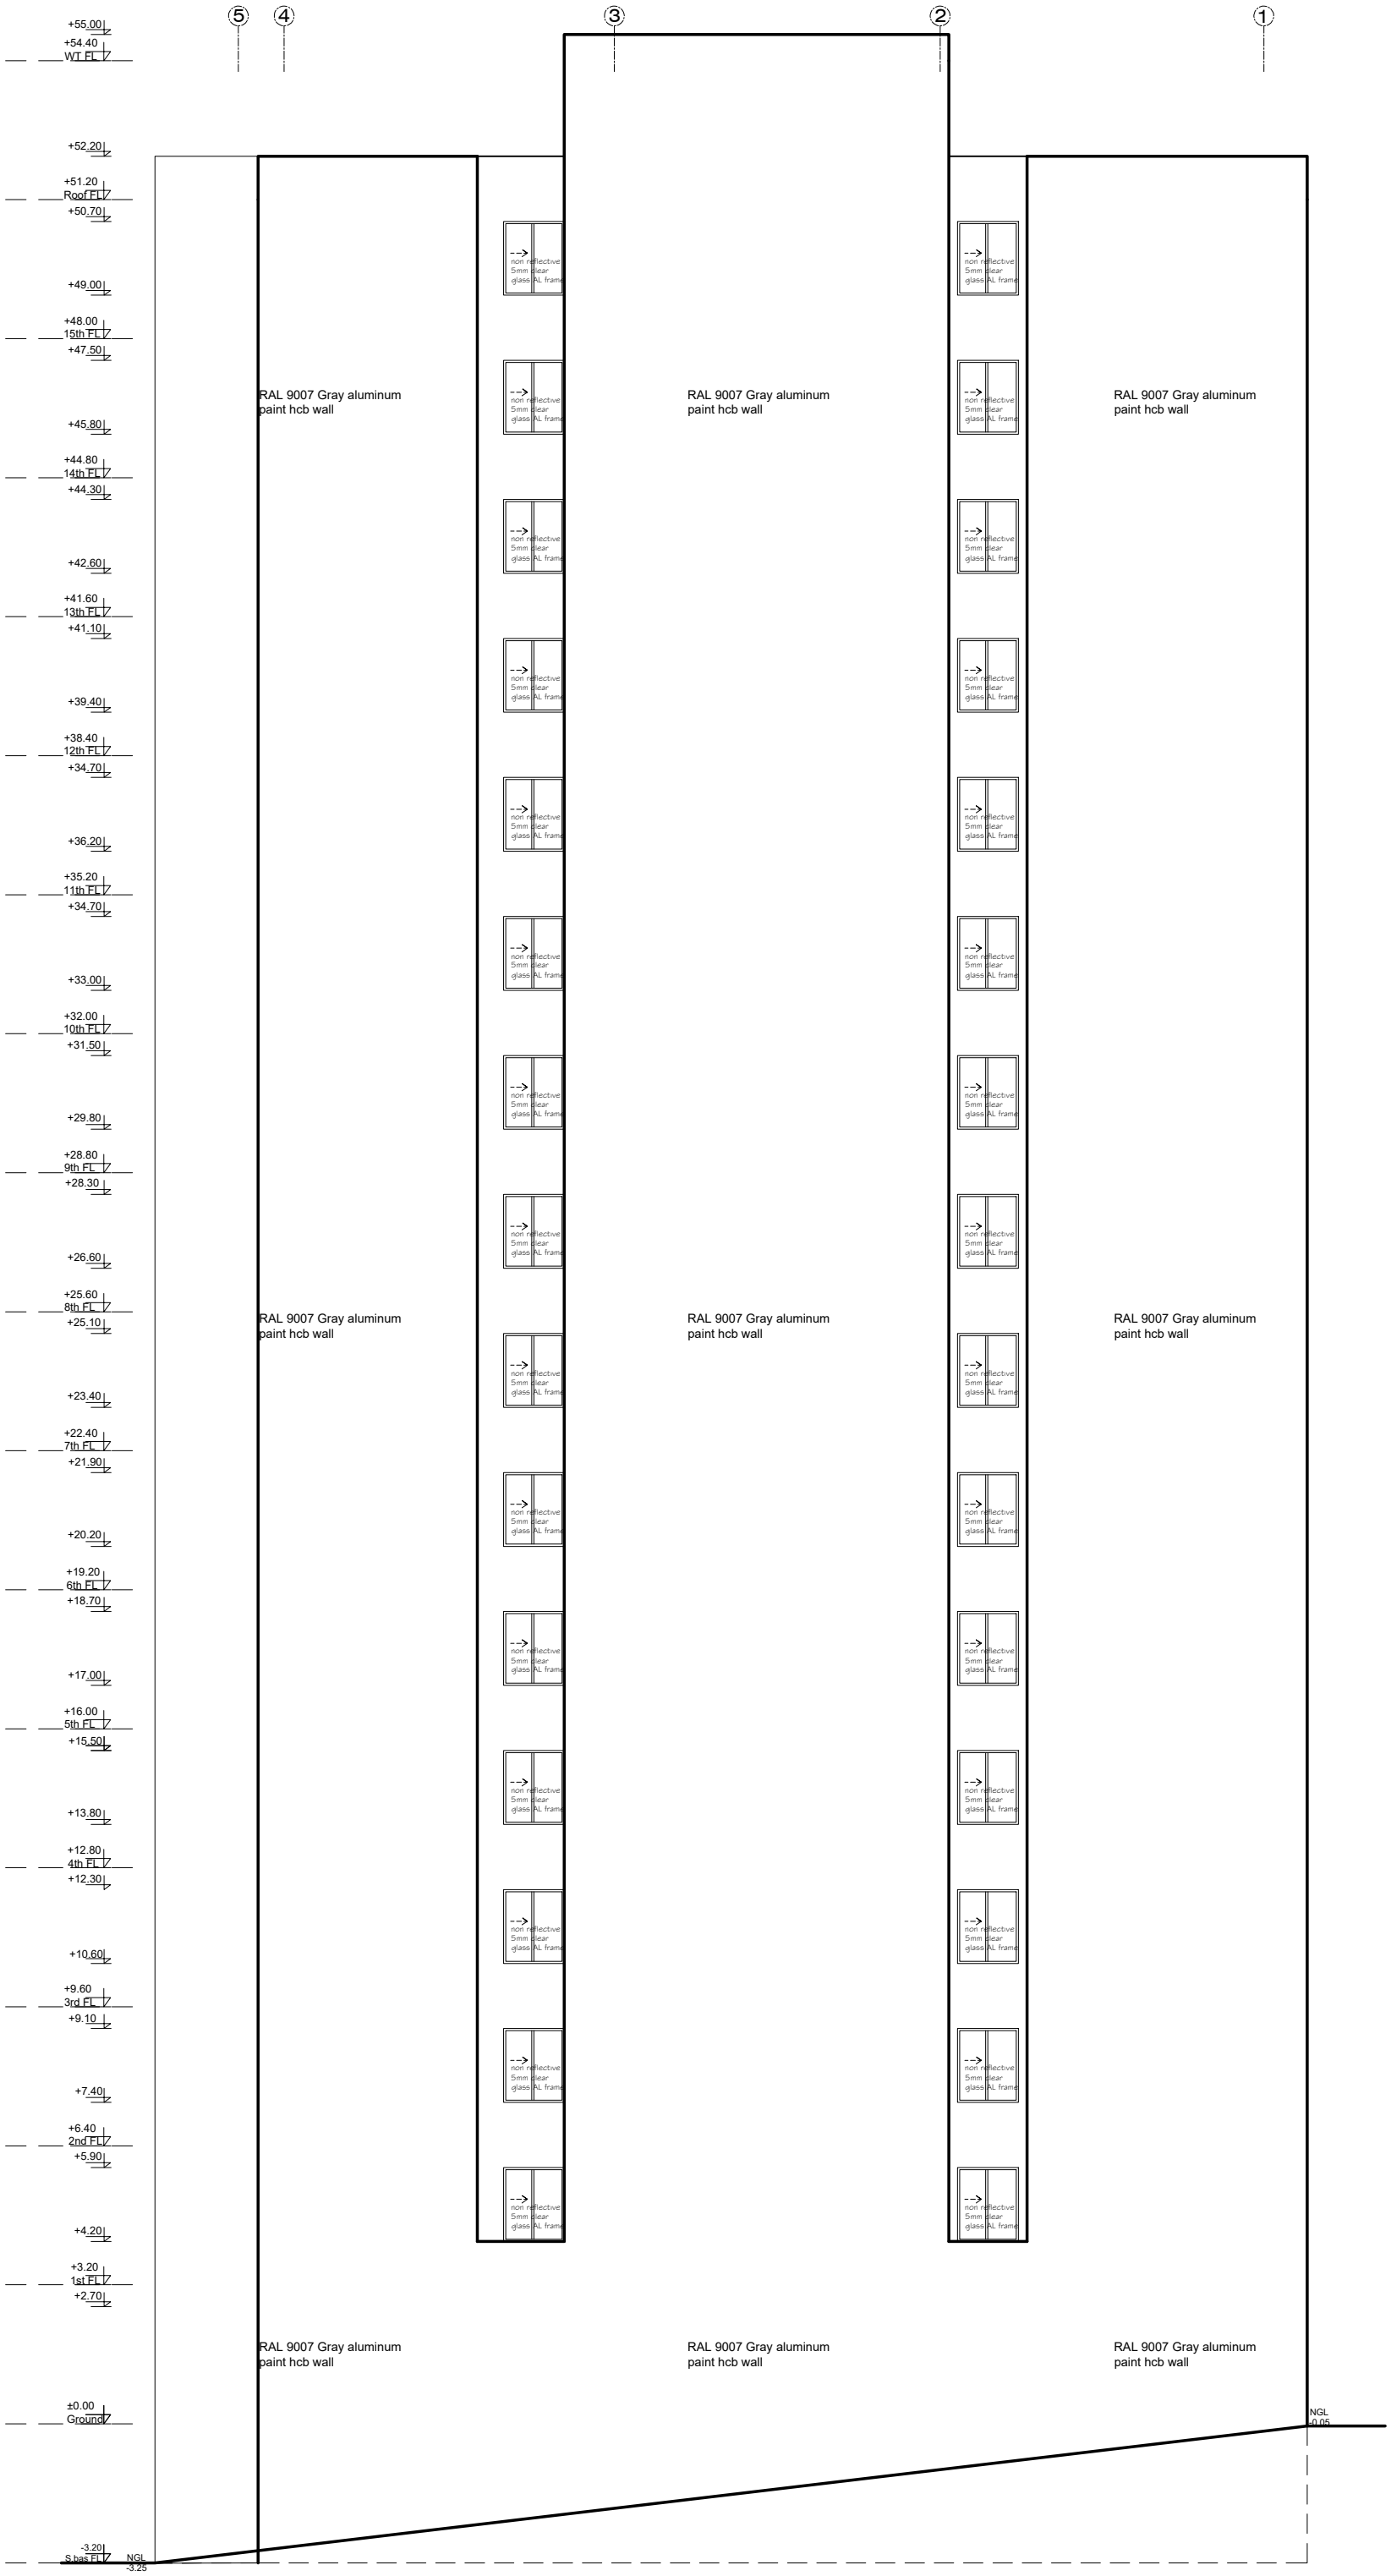

LEFT SIDE ELEVATION Scale 1:50

KDT DESIGN, DEVELOPMENT & TRADING PLC

Tel.+251-930-097319 ,+251-910-851364 ,+251-960-099854
Email- kdtdesign1@gmail.com

GRAY SHADE
Consulting Architects
Consulting Architects & Engineers

Tell. +251 911736607
Tell. +251 912354899
Po.Box 3209 code 1250
email. arefeaynej@gmail.com
Addis Ababa , Ethiopia

DESIGN STATUS


✓ NEW	MODIFICATION	AS-BUILT	CON.

PROJECT SB+G+15 APARTMENT BLDG

OWNER YO HART TRADING PLC


LOCATION
City, A.A, Subcity Yeka, Kebele , Woreda 08, House No
Title deed - AA000050802441 Parcel No. Area 422m²

DWG TTL		FILE NAME	
LEFT SIDE ELEVATION		1098	**AR**
DESIGN BY	CHECK	DRW	WORKING
AREFEAYNE B. PPAR 3208	A.B	Medhin W.	
	SCALE	DATE	DR.NO.
	AS INDICATED	SEP 2025	**08/11**

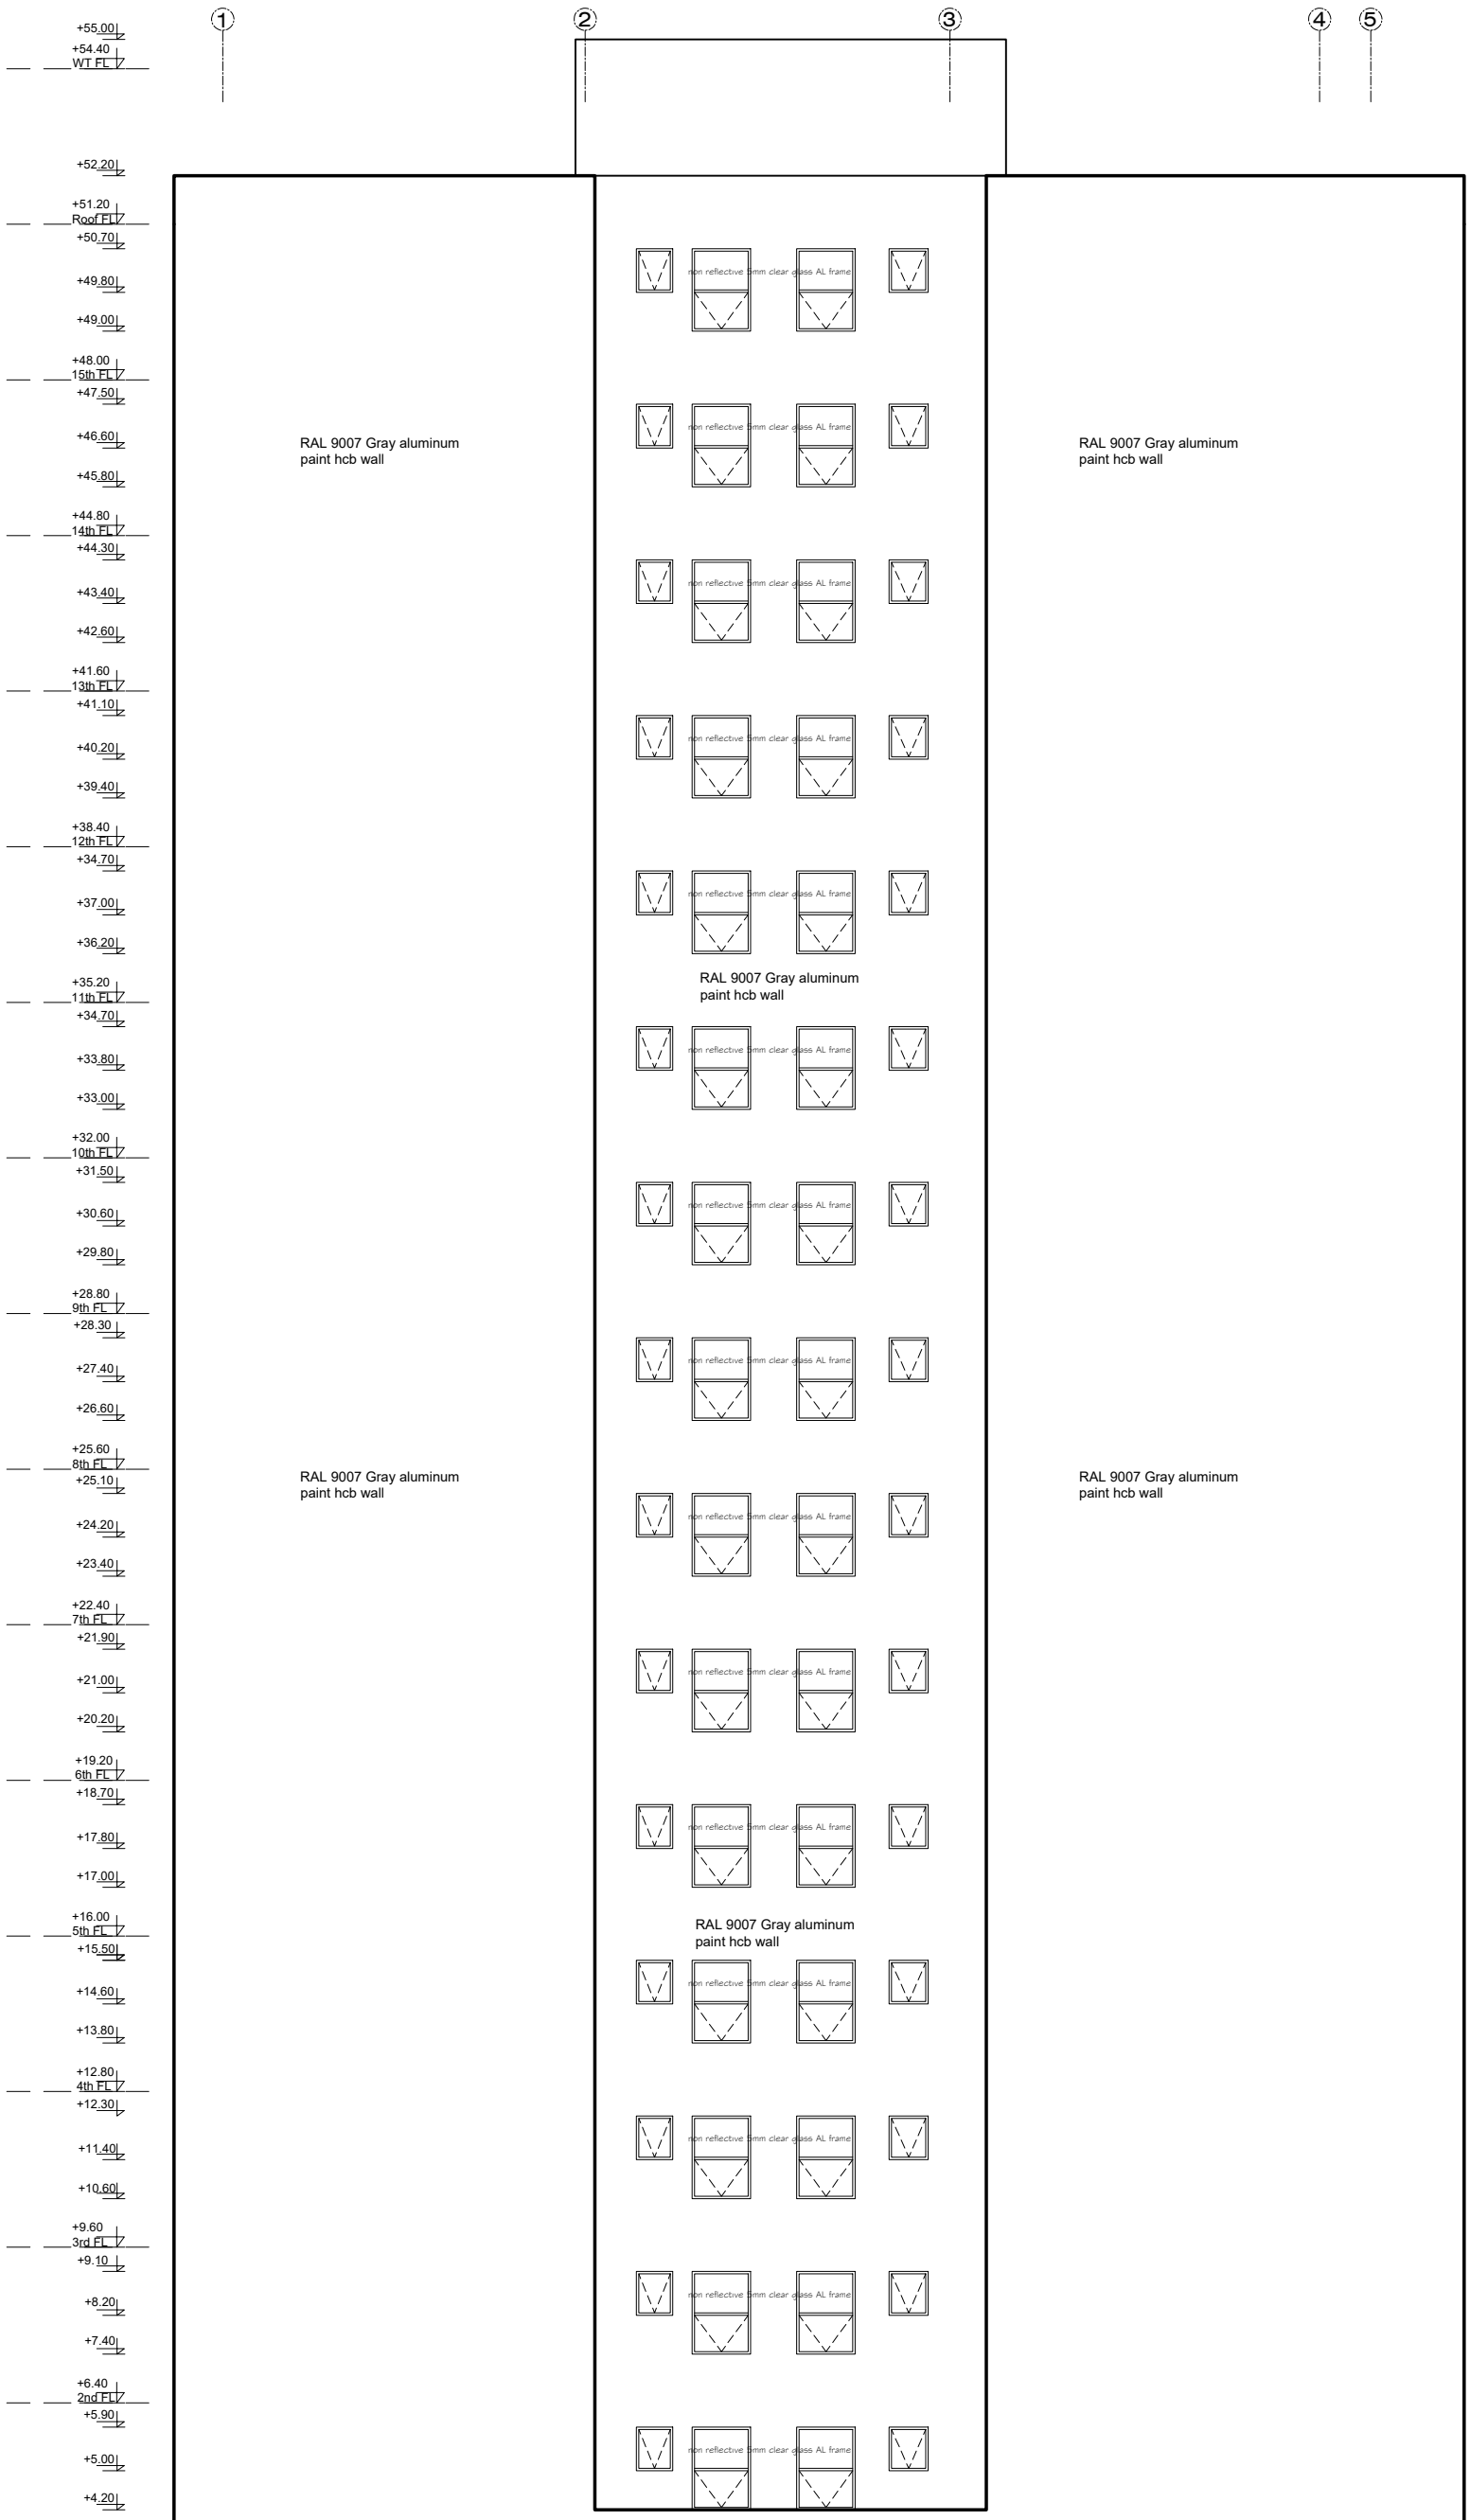


RIGHT SIDE ELEVATION Scale 1:50

KDT DESIGN, DEVELOPMENT & TRADING PLC	
Tel.+251-930-097319 ,+251-910-851364 ,+251-960-099854	
Email- kdtdesign1@gmail.com	
GRAY SHADE Consulting Architects Consulting Architects & Engineers	
Tell. +251 911736607 Tell. +251 912354899 Po.Box 3209 code 1250 email. arefeaynej@gmail.com Addis Ababa , Ethiopia	
DESIGN STATUS	✓ NEW ☐ MODIFICATION ☐ AS-BUILT ☐ CON.
PROJECT	SB+G+15 APARTMENT BLDG
OWNER	YO HART TRADING PLC
LOCATION	City, A.A, Subcity Yeka, Kebele , Woreda 08, House No Title deed - AA000050802441 Parcel No. Area 422m²
DWG TTL: RIGHT SIDE ELEVATION	FILE NAME: 1098
DESIGN BY: AREFEAYNE B. PPAR 3208	CHECK: A.B
DRW: Medhin W.	AR WORKING
SCALE: AS INDICATED	DATE: SEP 2025
DR.NO.: 09/11	

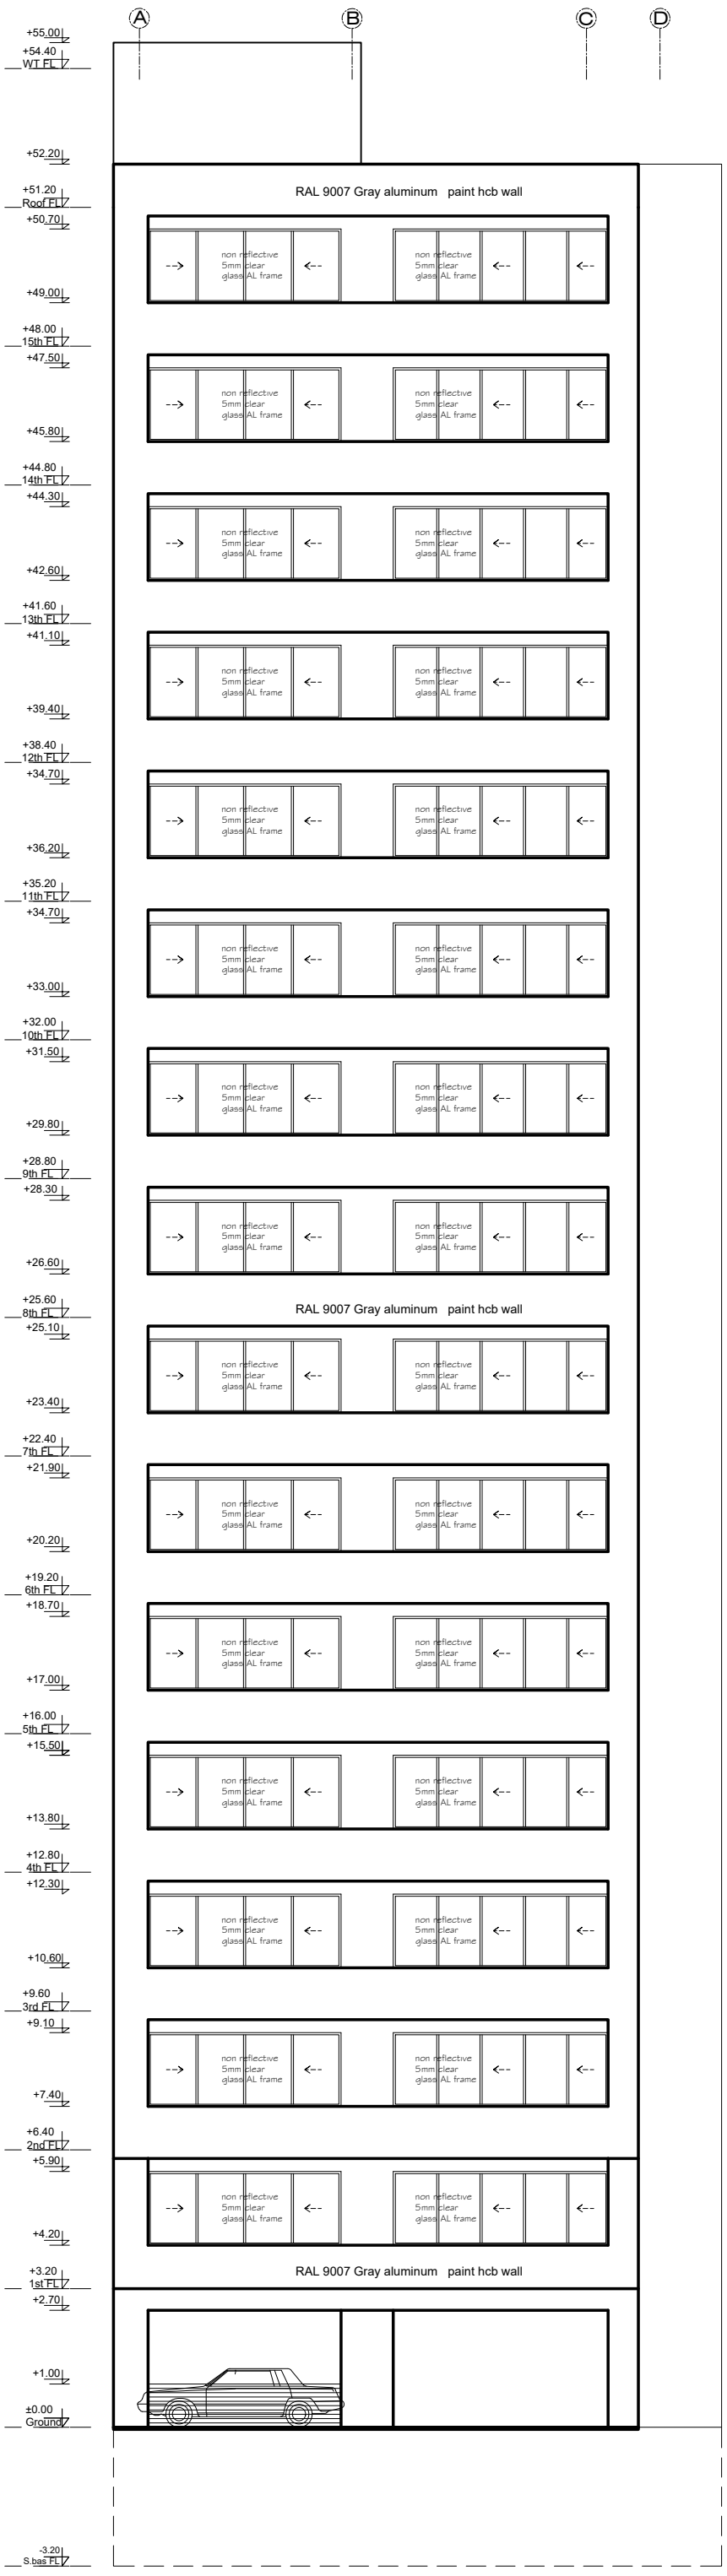

FRONT ELEVATION Scale 1:50

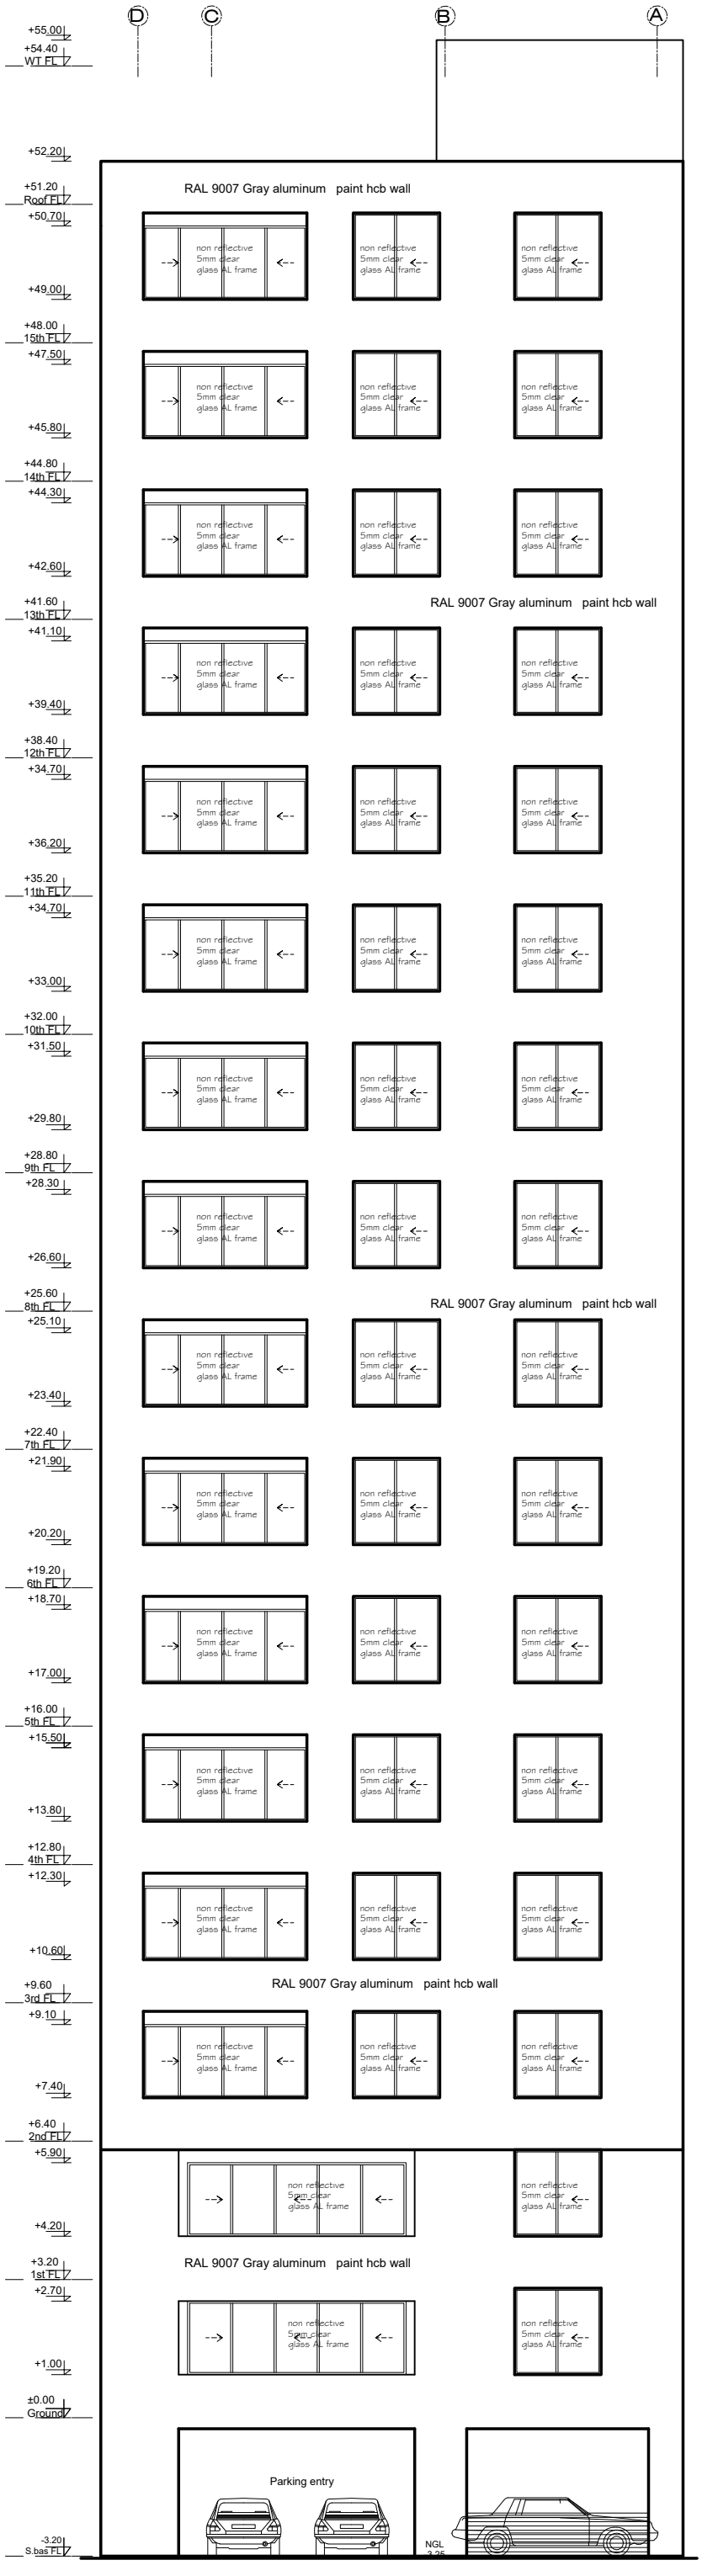

REAR SIDE ELEVATION Scale 1:50

KDT DESIGN, DEVELOPMENT & TRADING PLC

Tel.+251-930-097319 ,+251-910-851364 ,+251-960-099854
Email- kdtdesign1@gmail.com

GRAY SHADE
Consulting Architects
Consulting Architects & Engineers

Tell. +251 911736607
Tell. +251 912354899
Po.Box 3209 code 1250
email. arefeaynej@gmail.com
Addis Ababa , Ethiopia


DESIGN STATUS
[✓] NEW [ ] MODIFICATION [ ] AS-BUILT [ ] CON.

PROJECT SB+G+15 APARTMENT BLDG

OWNER YO HART TRADING PLC

LOCATION
City, A.A, Subcity Yeka, Kebele , Woreda 08, House No
Title deed - AA000050802441 Parcel No. Area 422m²

DWG TTL: FRONT AND REAR SIDE ELEVATION		FILE NAME: 1098	AR
DESIGN BY: AREFEAYNE B. PPAR 3208	CHECK: A.B	DRW: Medhin W.	WORKING
	SCALE: AS INDICATED	DATE: SEP 2025	DR.NO. 10/11

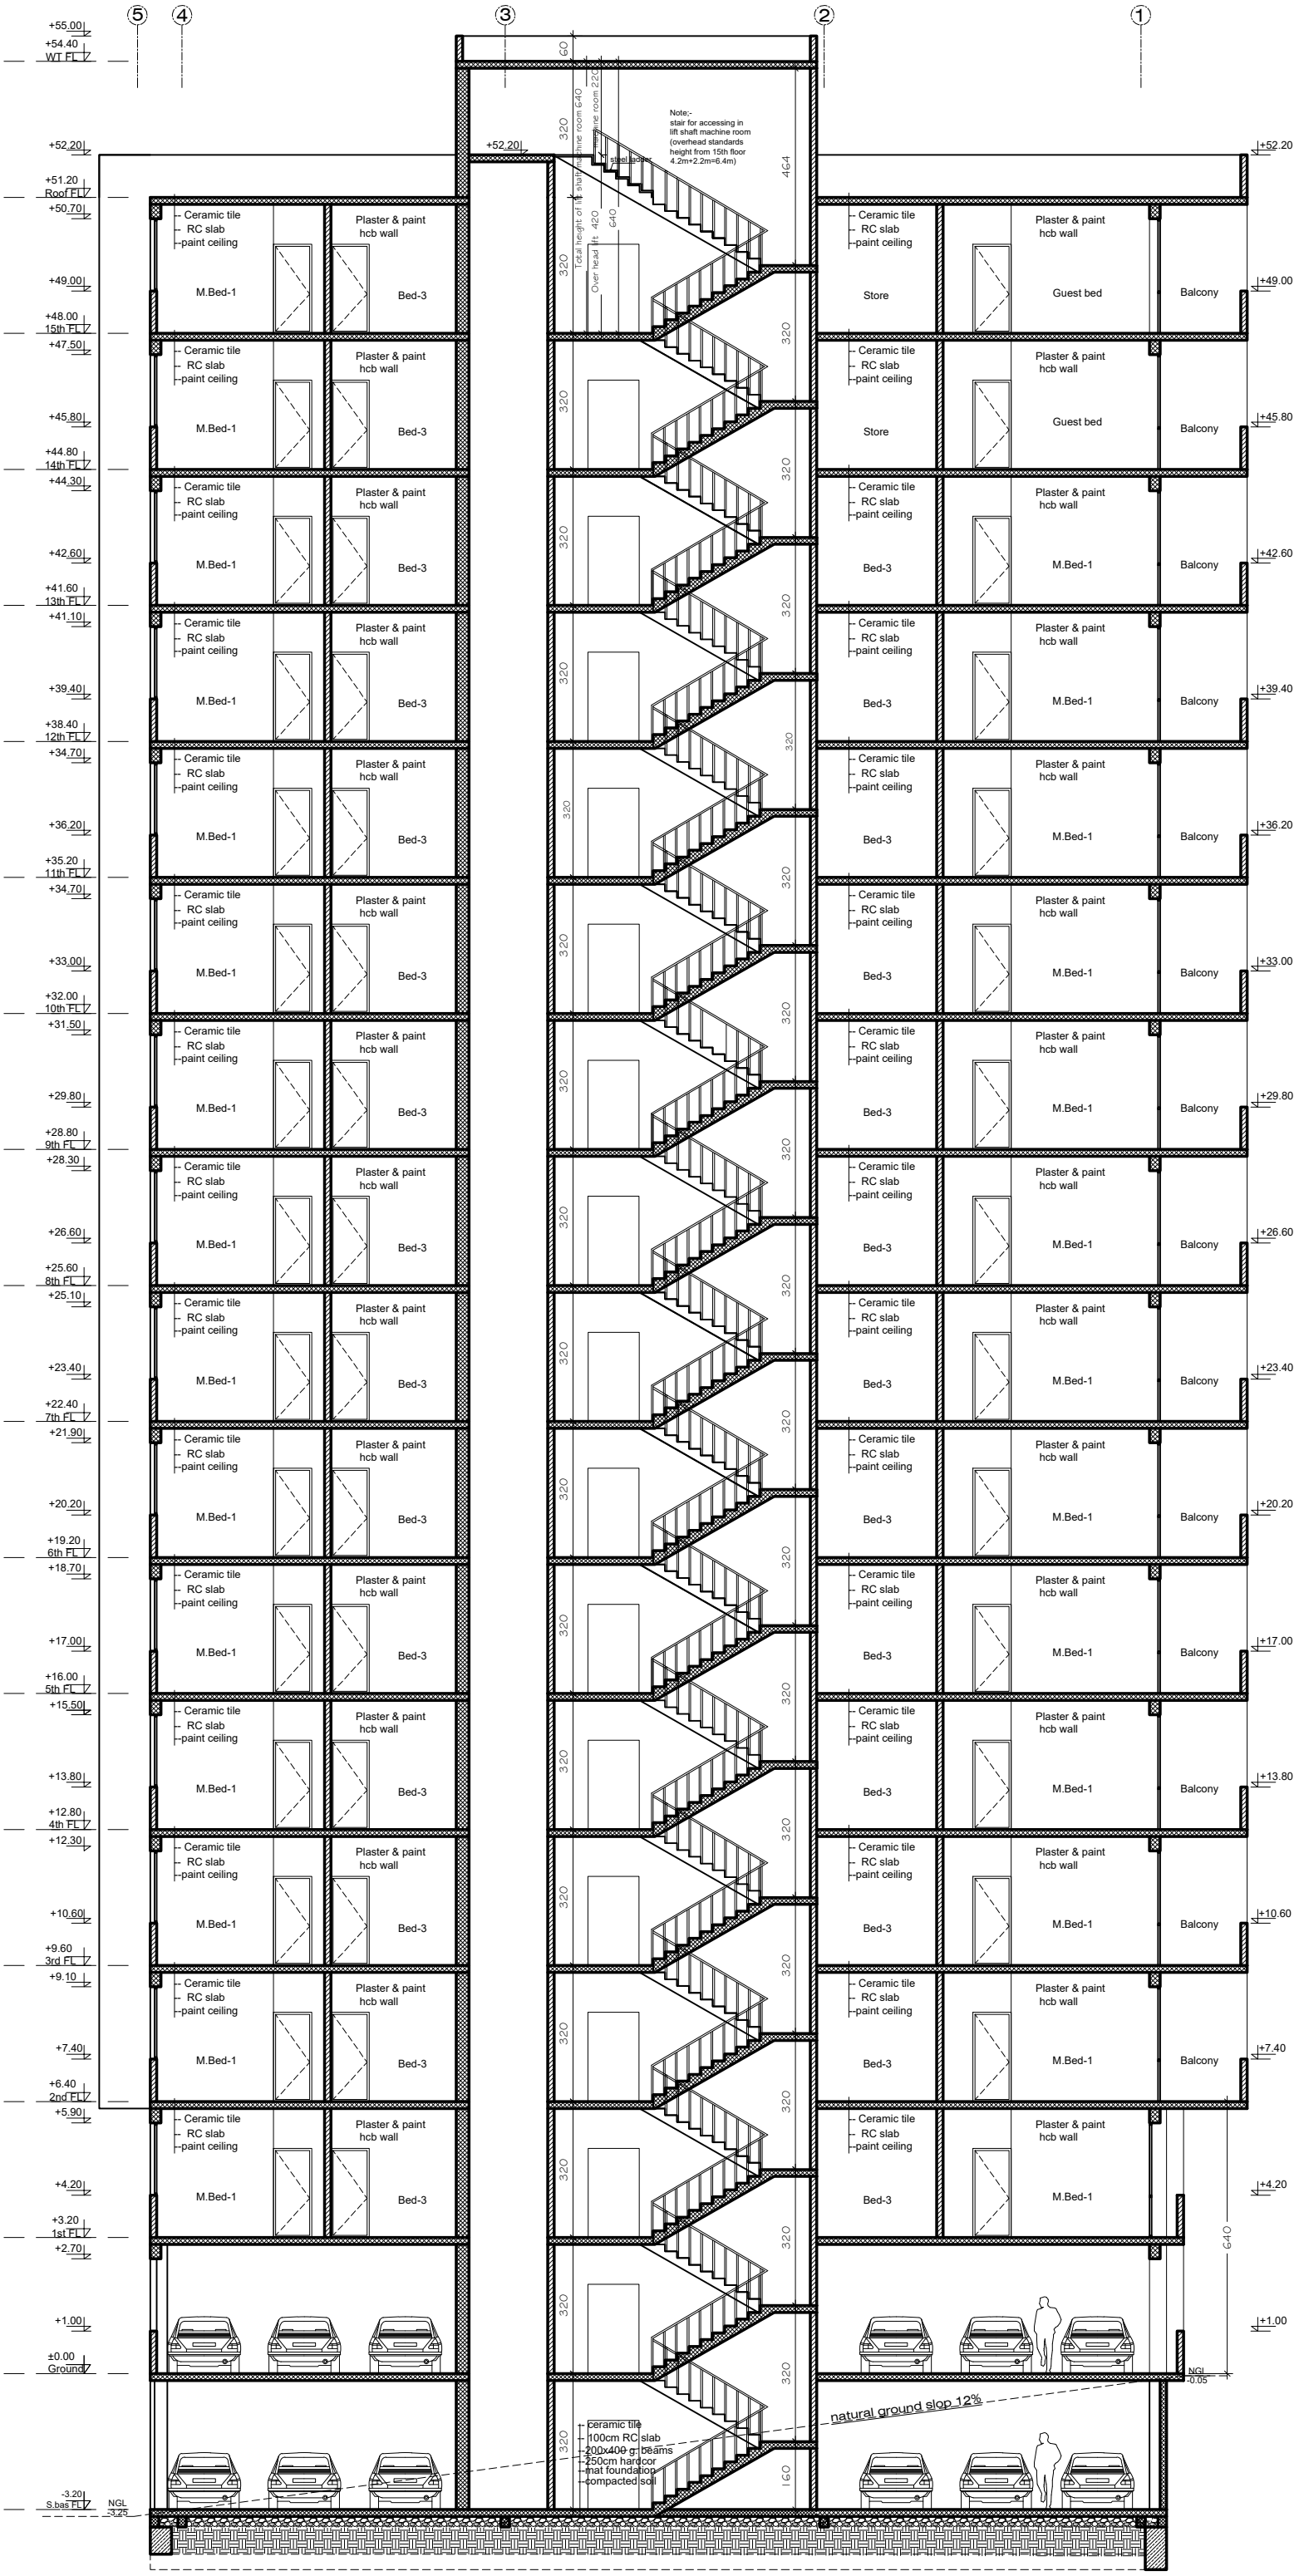

SECTION 1-1 SC 1:50

KDT DESIGN, DEVELOPMENT & TRADING PLC

Tel.+251-930-097319 ,+251-910-851364 ,+251-960-099854
Email- kdtdesign1@gmail.com

GRAY SHADE
Consulting Architects
Consulting Architects & Engineers

Tell. +251 911736607
Tell. +251 912354899
Po.Box 3209 code 1250
email. arefeaynej@gmail.com
Addis Ababa , Ethiopia

DESIGN STATUS: ✓ NEW | MODIFICATION | AS-BUILT | CON.

PROJECT: SB+G+15 APARTMENT BLDG

OWNER: YO HART TRADING PLC

LOCATION: City, A.A, Subcity Yeka, Kebele , Woreda 08, House No
Title deed - AA000050802441 Parcel No. Area 422m²

DWG TTL: SECTION		FILE NAME: 1098	AR
DESIGN BY: AREFEAYNE B. PPAR 3208	CHECK: A.B	DRW: Medhin W.	WORKING
	SCALE: AS INDICATED	DATE: SEP 2025	DR.NO. 11/11